



Stephanie & Kevin House

Atelier Vens Vanbelle

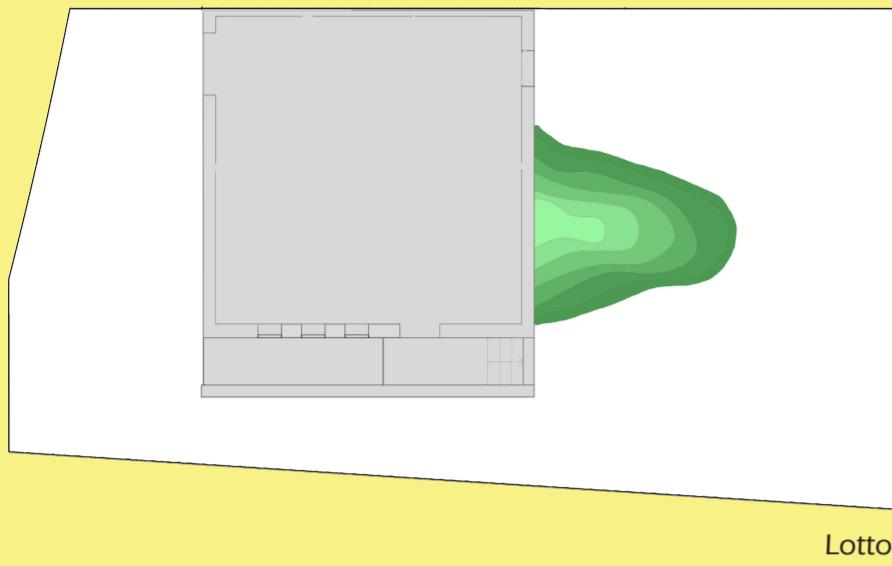


Lotto


La casa di 185 m² è stata progettata da Atelier Vens Vanbelle nel 2016 ed è situata a Haaltert, Belgio. L'edificio si trova alla fine di una strada senza uscita, accanto all'edificio il paesaggio inizia a declinare e si può godere di una bellissima vista. Sul lato e sul retro dell'edificio vi è un sentiero che viene usato sporadicamente dagli escursionisti. La posizione della casa è particolarmente favorevole poiché vi è il sole tutto il giorno e la casa risulta sempre illuminata.

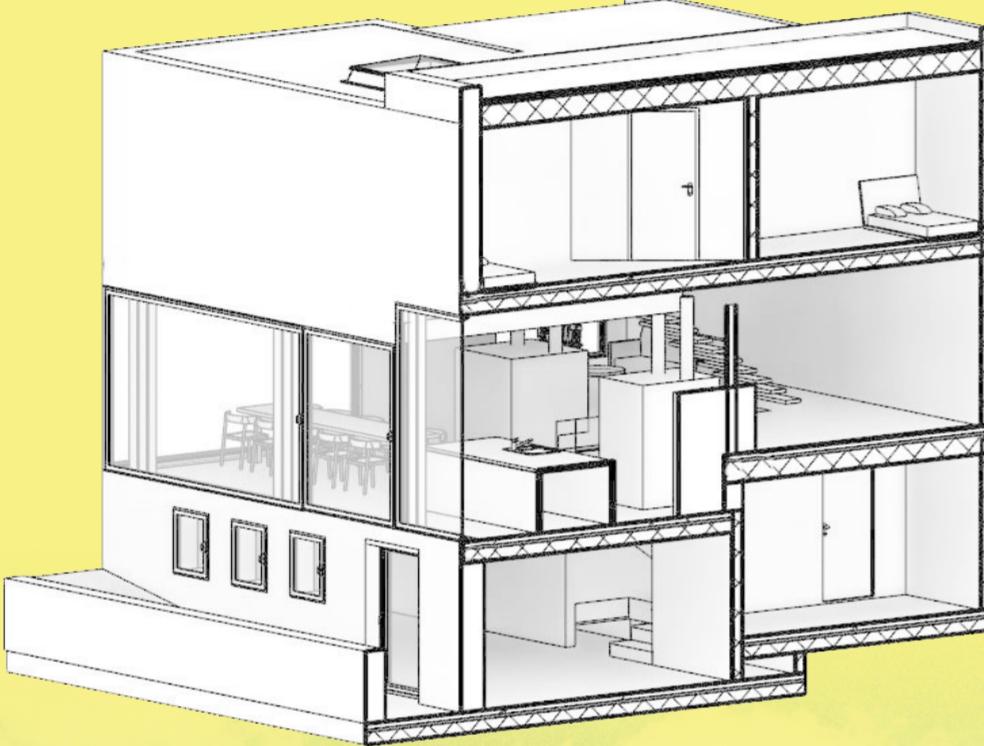


La casa è costruita su livelli diversi e ciò permette di creare intriganti relazioni tra i vari spazi. Lo spazio abitativo è fornito al primo piano, su un volume di blocchi di cemento. All'interno di questo basamento c'è uno spazioso seminterrato / workstudio semi-sotterraneo; mezzo livello più in alto - al piano terra - c'è un ingresso esterno coperto, un ingresso e un ripostiglio / lavanderia. Lo spazio abitativo è concepito come un palcoscenico verso l'ambiente. Lo spazio è vetrato su tre lati, quindi il sole arriva tutto il giorno e ti dà la sensazione di essere a stretto contatto con l'ambiente.

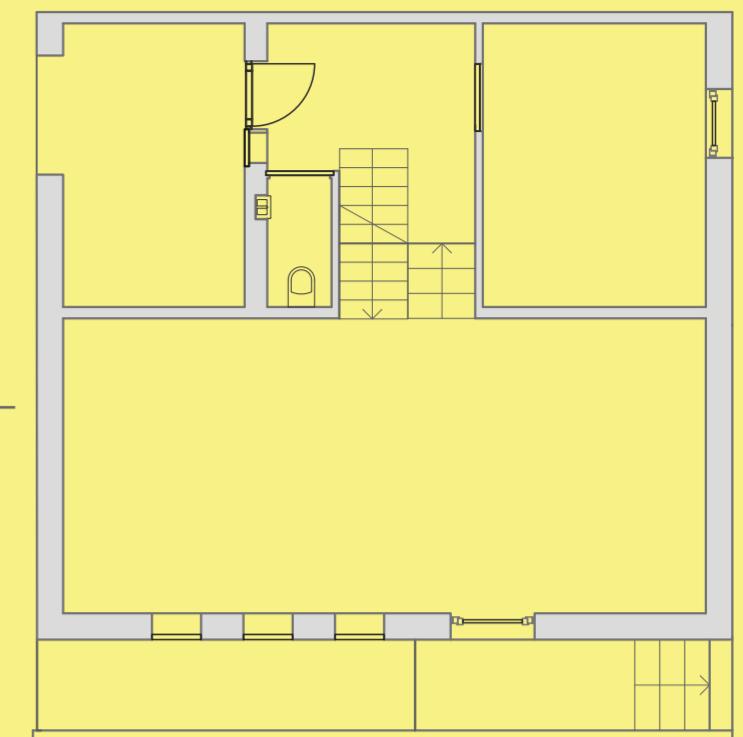

Pianta Piano Terra Scala 1:100





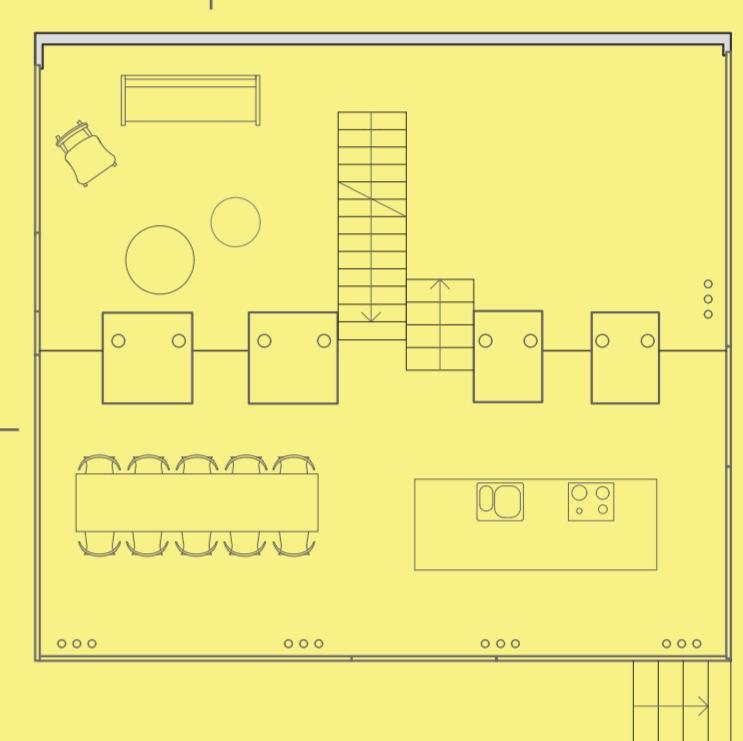


Pianta Primo Piano Scala 1:100

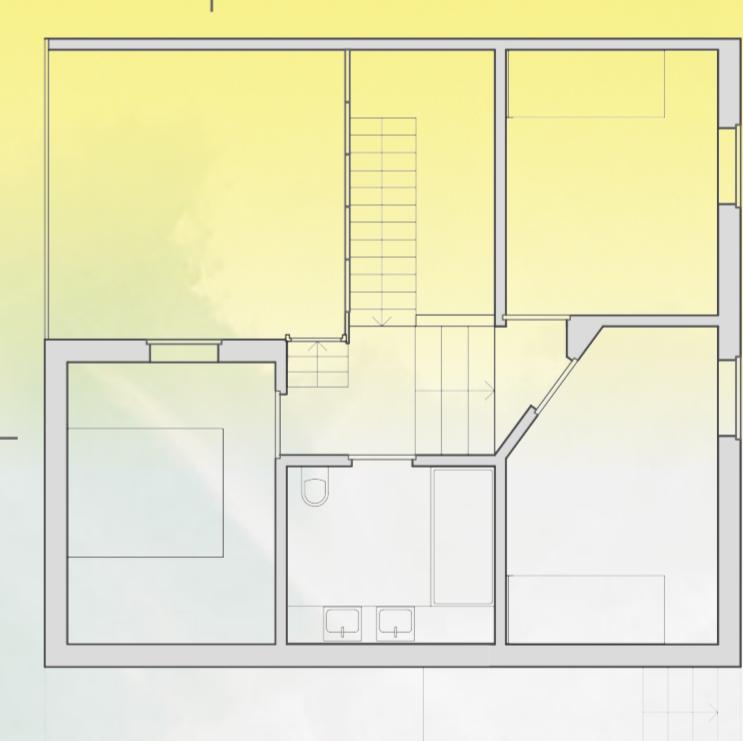


Pianta Secondo Piano Scala 1:100



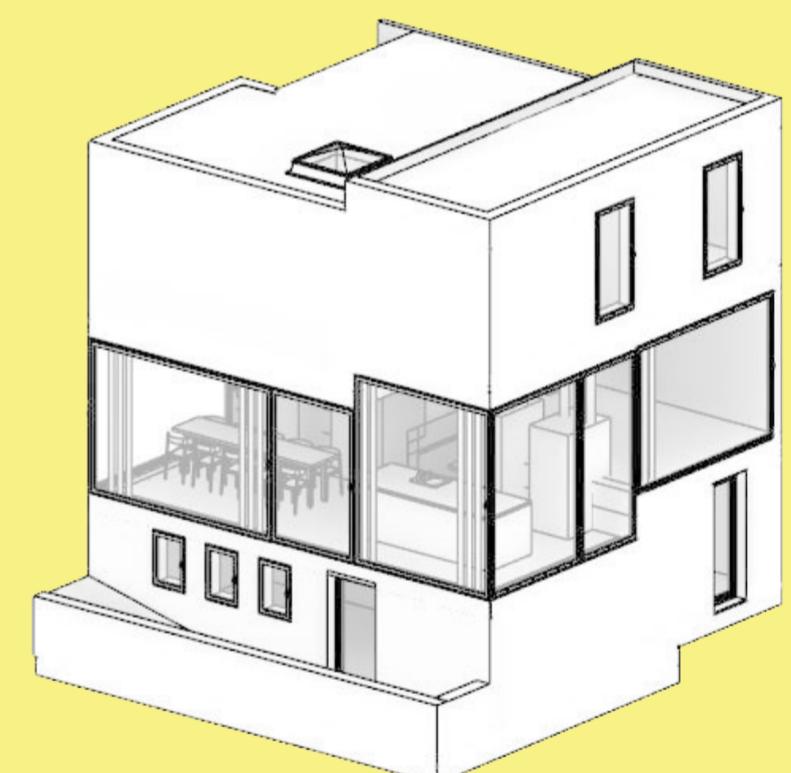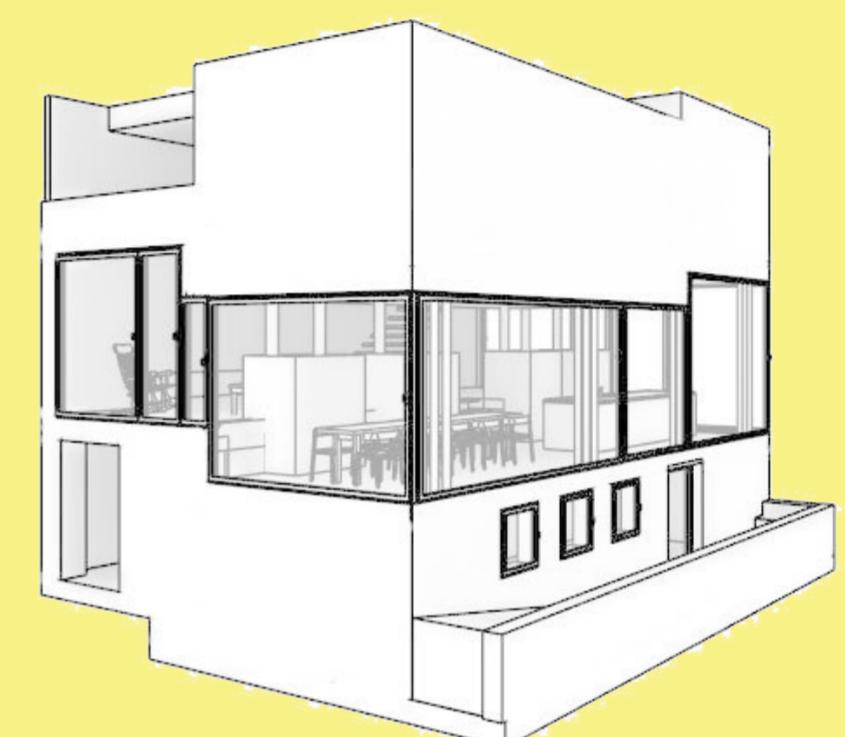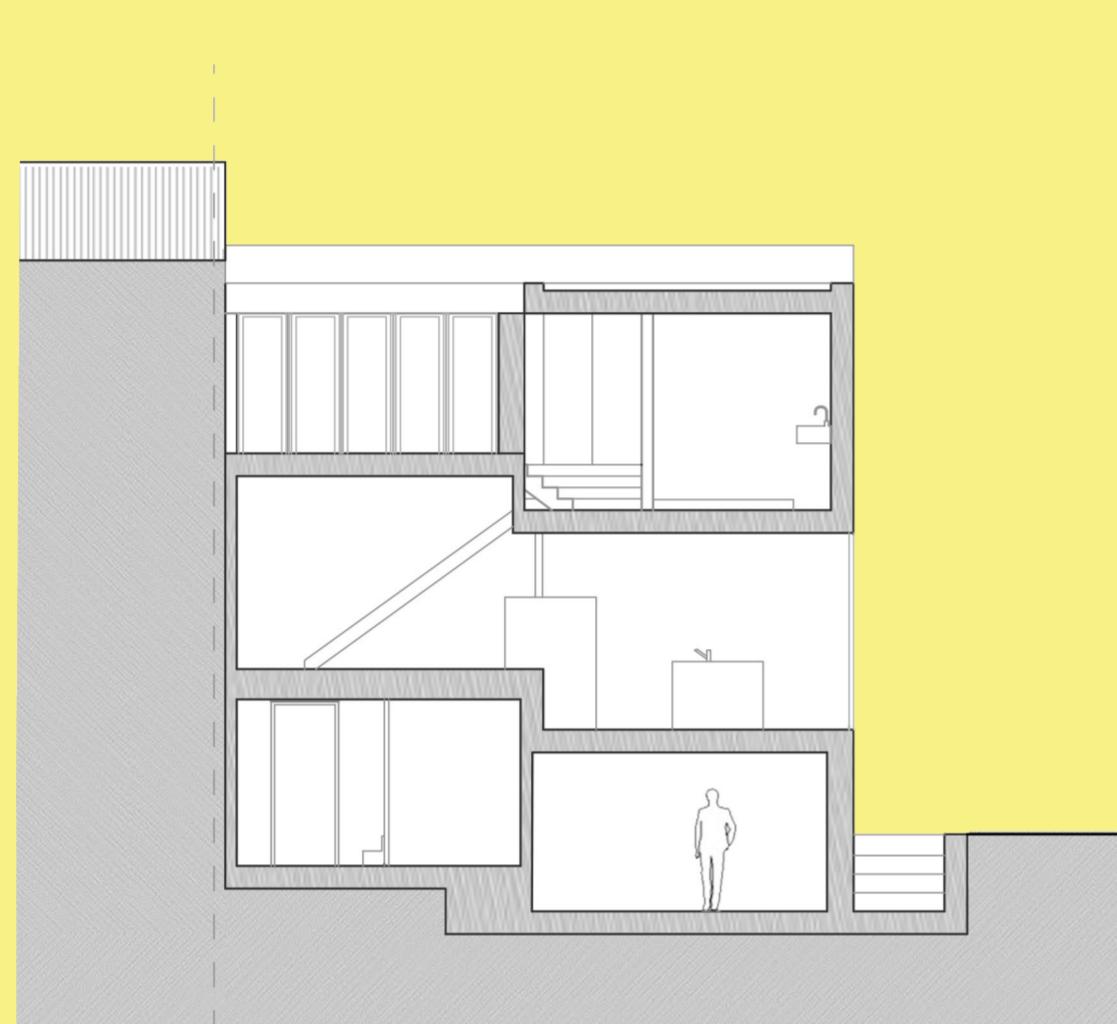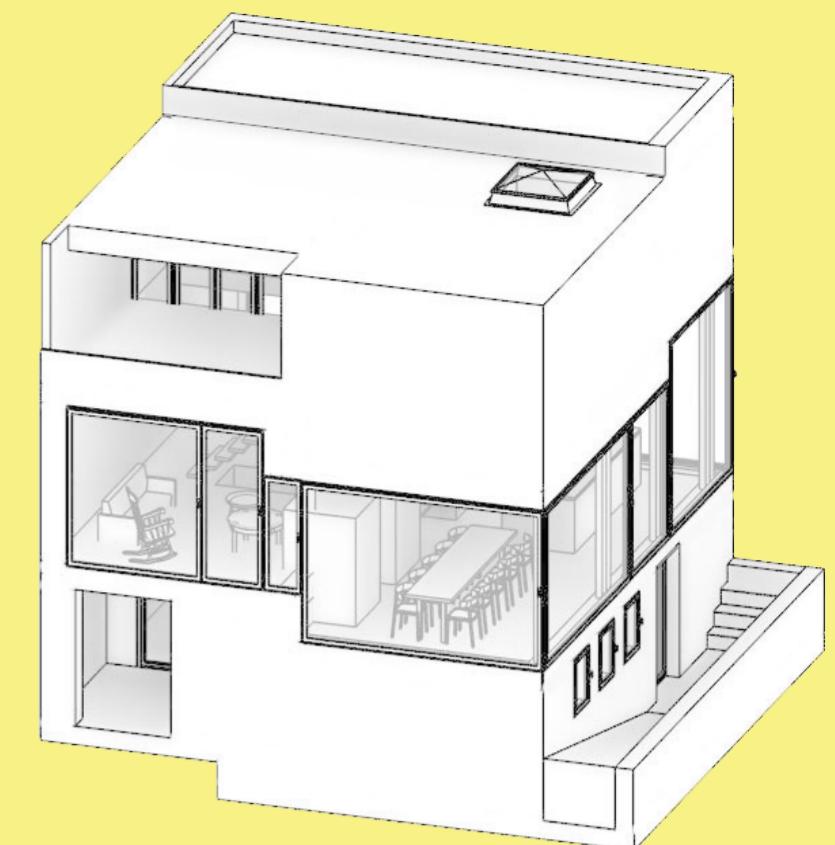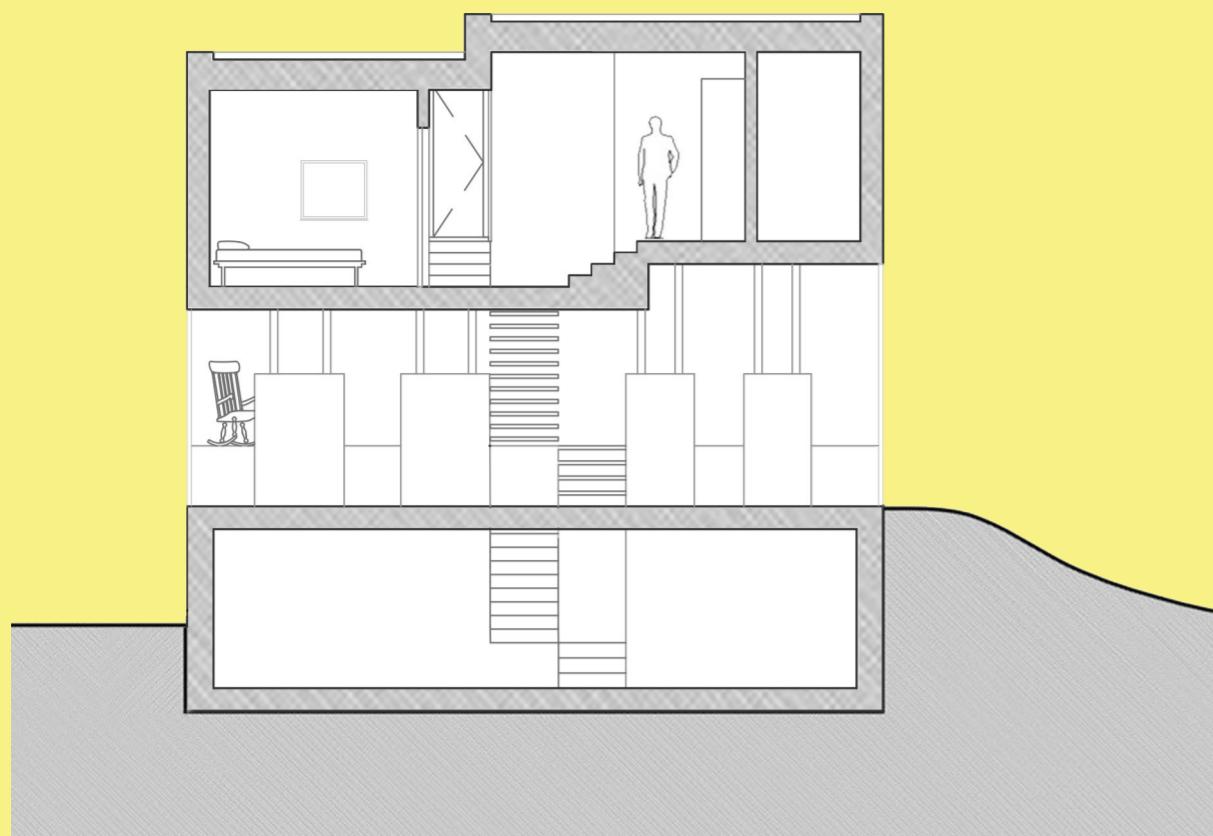

Per fornire l'intimità necessaria a questo spazio, sia il pavimento che le pareti e i soffitti sono stati rivestiti con parquet. Quattro armadi sono stati collocati nel mezzo del soggiorno sia perché funzionali ma al tempo stesso forniscono privacy nell'area salotto. Le sottili colonne che portano il volume giallo chiuso formano anche un sottile cuscinetto per l'ambiente. È uno spazio che si bilancia perfettamente tra aperto e chiuso. Tre camere da letto e un bagno sono stati integrati nel volume giallo. Dal corridoio aperto è possibile accedere alla terrazza sul tetto. Attraverso la finestra accanto alla terrazza, la luce del sole entra nelle profondità della casa. Il volume edilizio si materializza molto facilmente, in modo che anche la stratificazione dell'edificio sia leggibile dall'esterno. C'è un dialogo tra la casa e il suo ambiente che rende la vita quotidiana interattiva senza compromettere il senso di privacy.

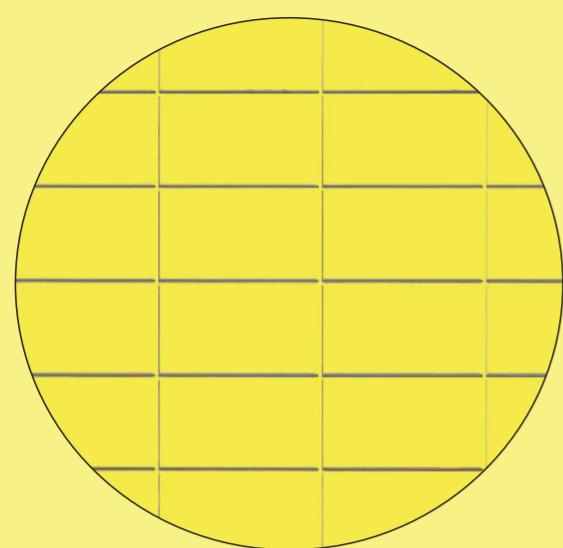

Piastrelle 10 x 25 giallo acceso
PANTONE 101 C



Prospetto Sud Scala 1:100




Mattoni 20 x 47 grigio caldo
PANTONE 420 C



Prospetto Nord Scala 1:100



Parquet di rovere naturale
PANTONE 729 C

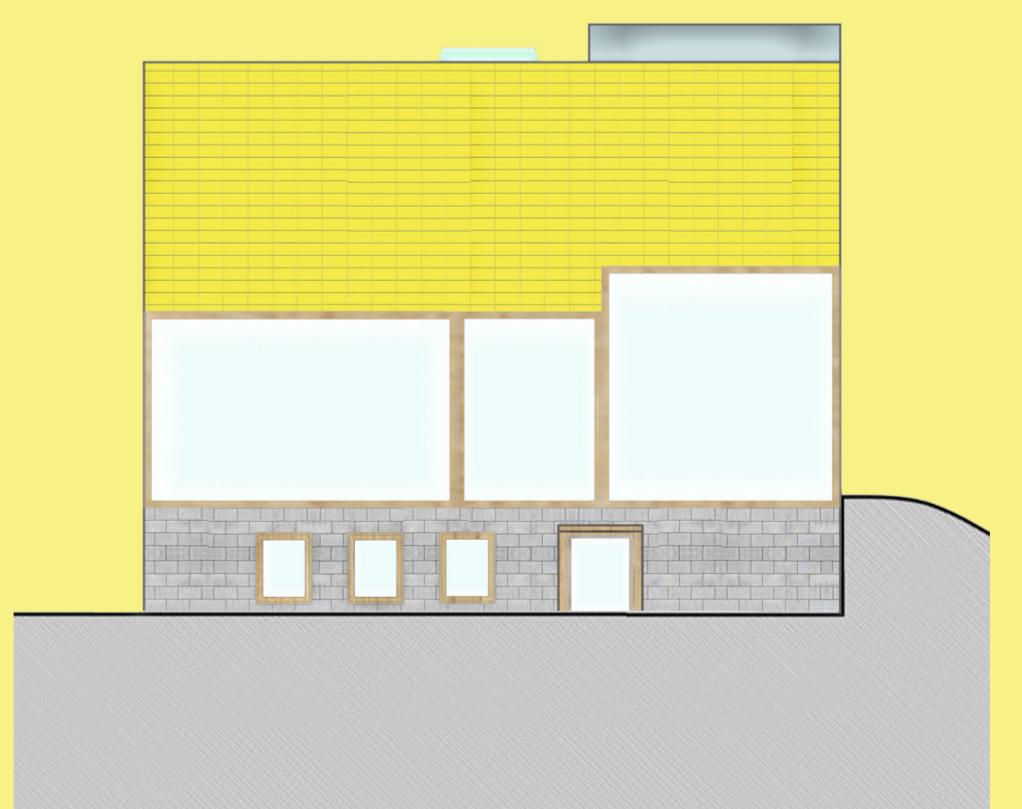

Prospetto Est Scala 1:100