


KONAN HOUSE

By ALTS Design Office


L'abitazione, realizzata nel 2017 dal gruppo ALTS Design Office, è situata a Koka, in Giappone. La particolarità della Konan House è lo spazio anteriore, dove il tetto è stato prolungato fino a coprire una pedana di legno appena fuori il soggiorno per realizzare uno spazio "quasi esterno", a stretto contatto con la natura. L'escamotage del tetto ha inoltre risolto il problema della copertura di questo ambiente, evitando il problema di montare una tenda. La struttura della casa è infatti ispirata al "Glamping resort" che offre ai visitatori uno spazio per sfuggire alla vita quotidiana e godersi la vita all'aria aperta.

La casa è costituita da due piani. Un tipico ingresso giapponese, dove sfilarsi le scarpe, precede l'entrata della casa ed è collegata ad un armadio. Il piano terra si presenta quasi interamente come un open-space ed è formato da un ampio soggiorno con cucina, tutto volto all'esterno grazie a una grande parete vetrata da cui è possibile anche uscire nello spazio prima descritto, e da un bagno distribuito su tre piccoli ambienti collegati tra loro.

Al piano superiore si trova un grazioso atrio e le due camere da letto, la padronale presenta anche un'ampia cabina armadio dove è contenuto il tatami. Tutto nella casa è realizzato con materiali dal colore neutro, in particolare il legno chiaro, a rendere lo spazio minimal.

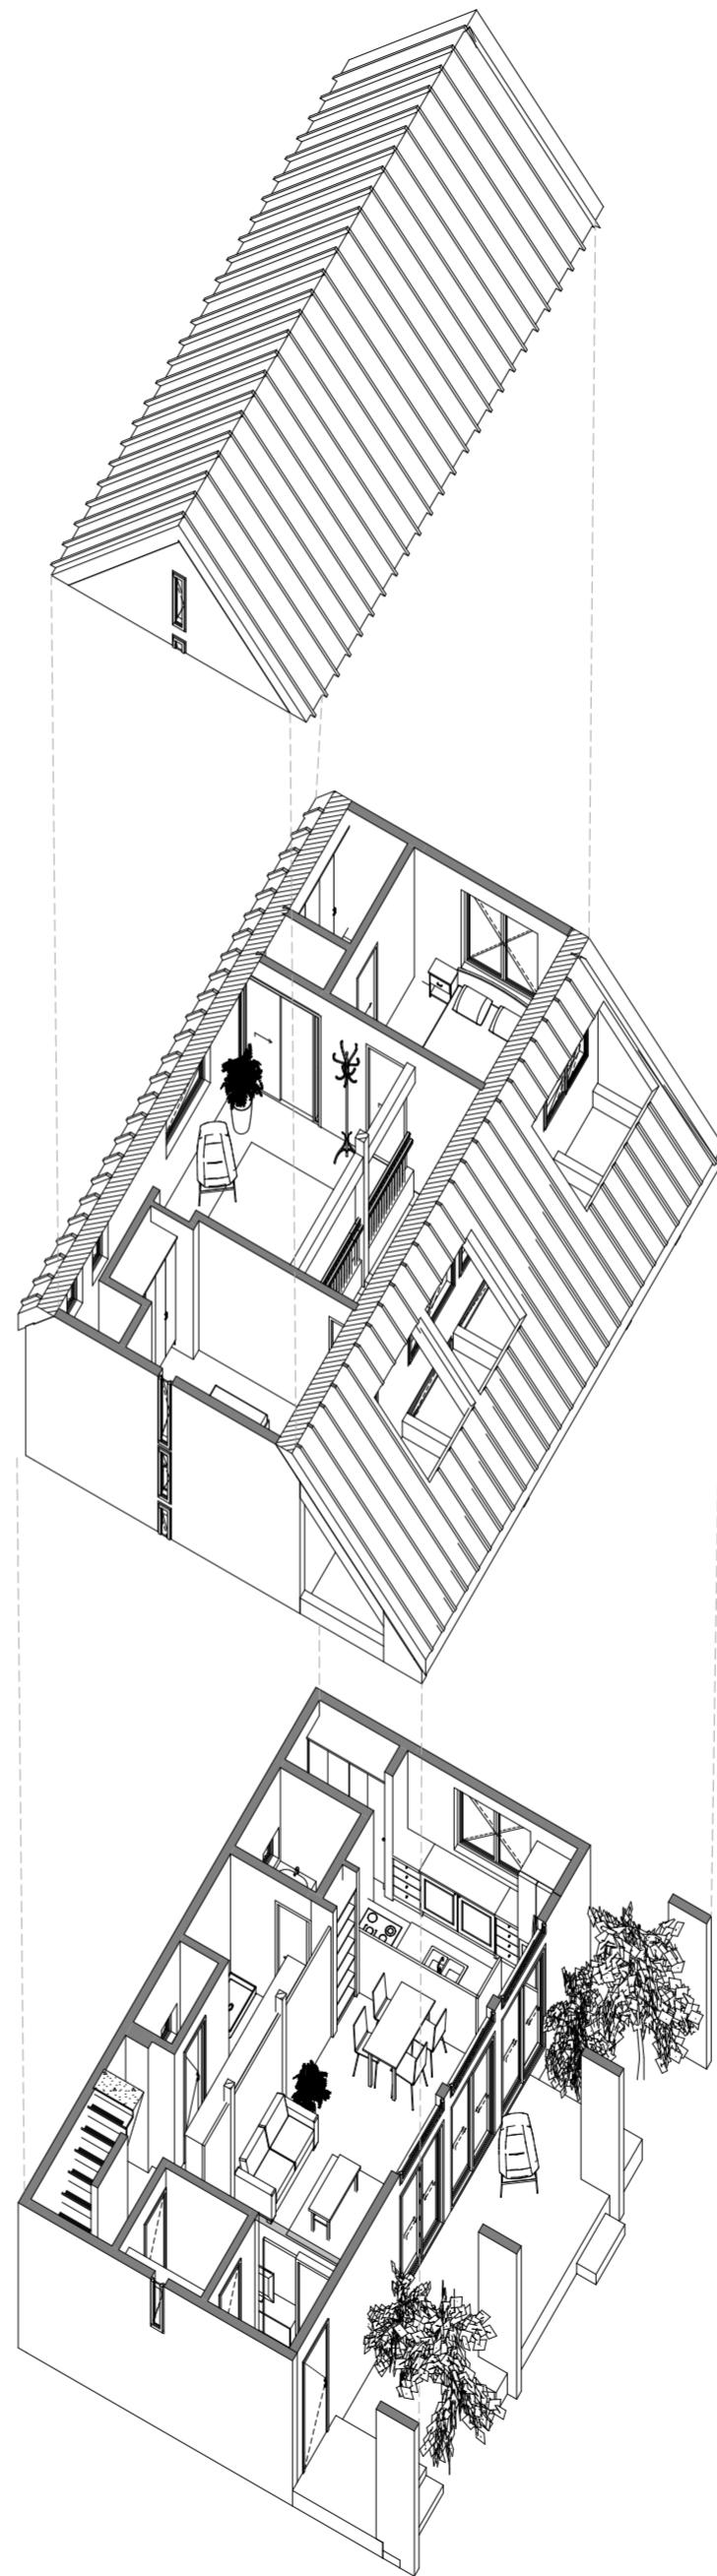


Esploso assonometrico

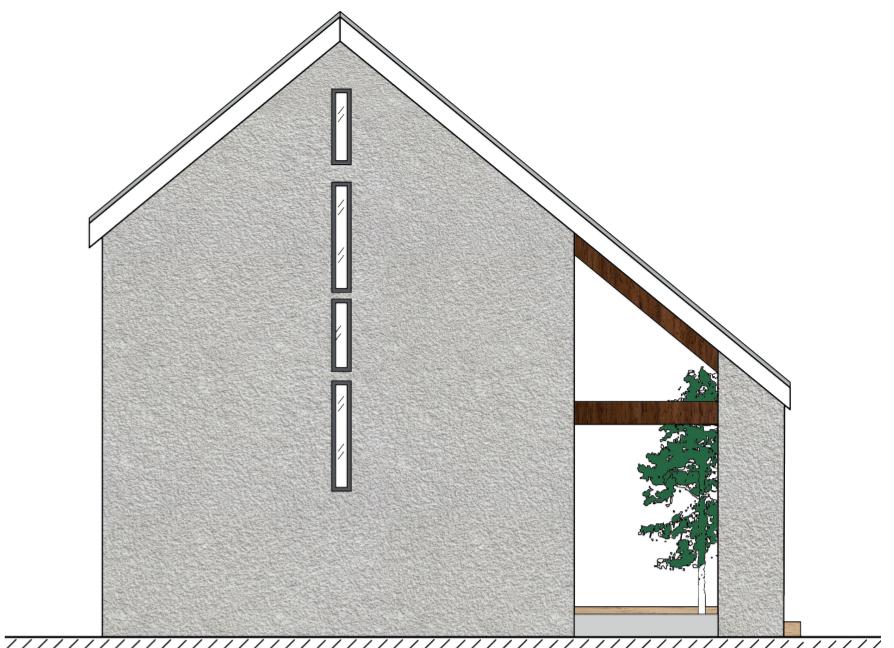


Prospetto sud scala 1:100



Prospetto est scala 1:100

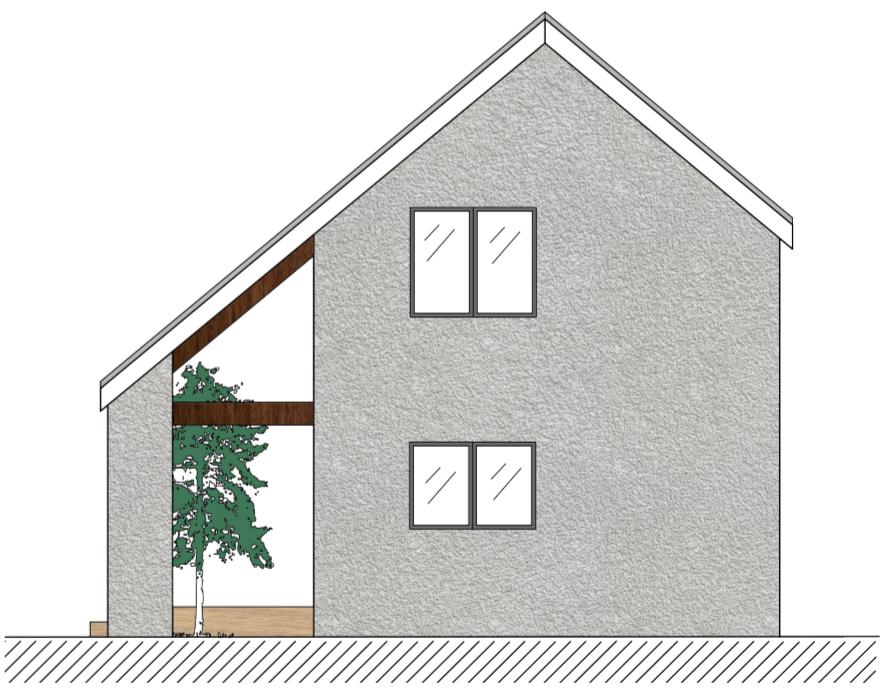

Prospetto nord scala 1:100

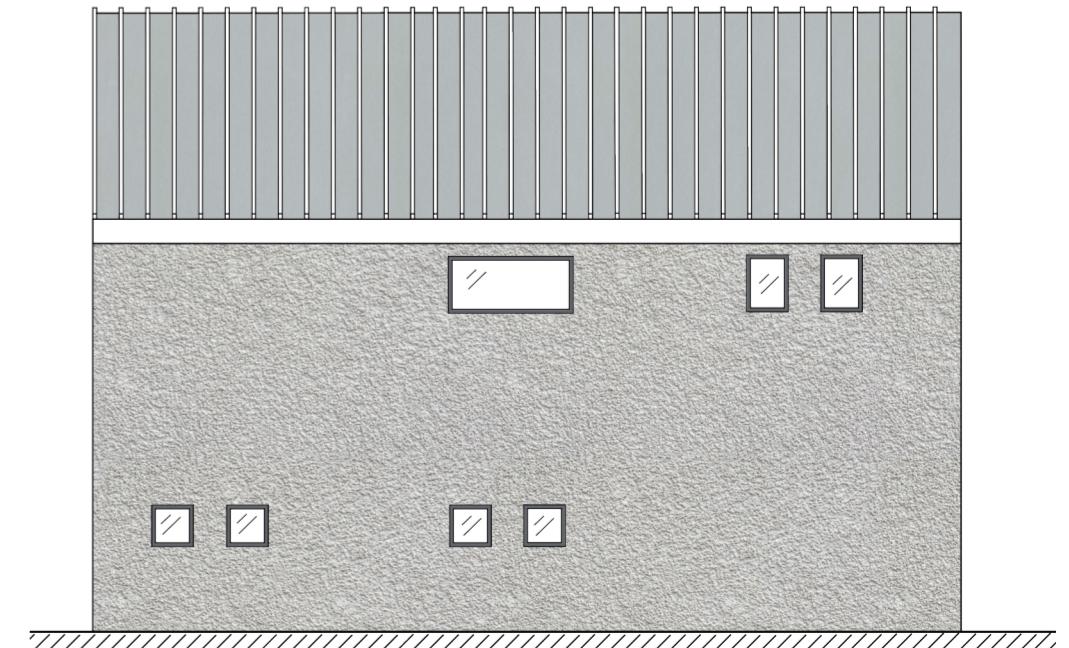

Prospetto ovest scala 1:100



KONAN HOUSE

By ALTS Design Office




Viste dell' interno: soggiorno e cucina con ampie vetrate sul giardino. Visibili i colori e le forme neutre, la buona esposizione alla luce di cui gode la casa, e la stretta connessione con l'esterno. La cucina è separata dal resto del soggiorno da una bassa parete di legno chiaro che riprende le tonalità di spicco dell'abitazione.

Laboratorio di Strumenti e Metodi del Progetto
Aurora Antonini Cencicchio, Aurora Serra

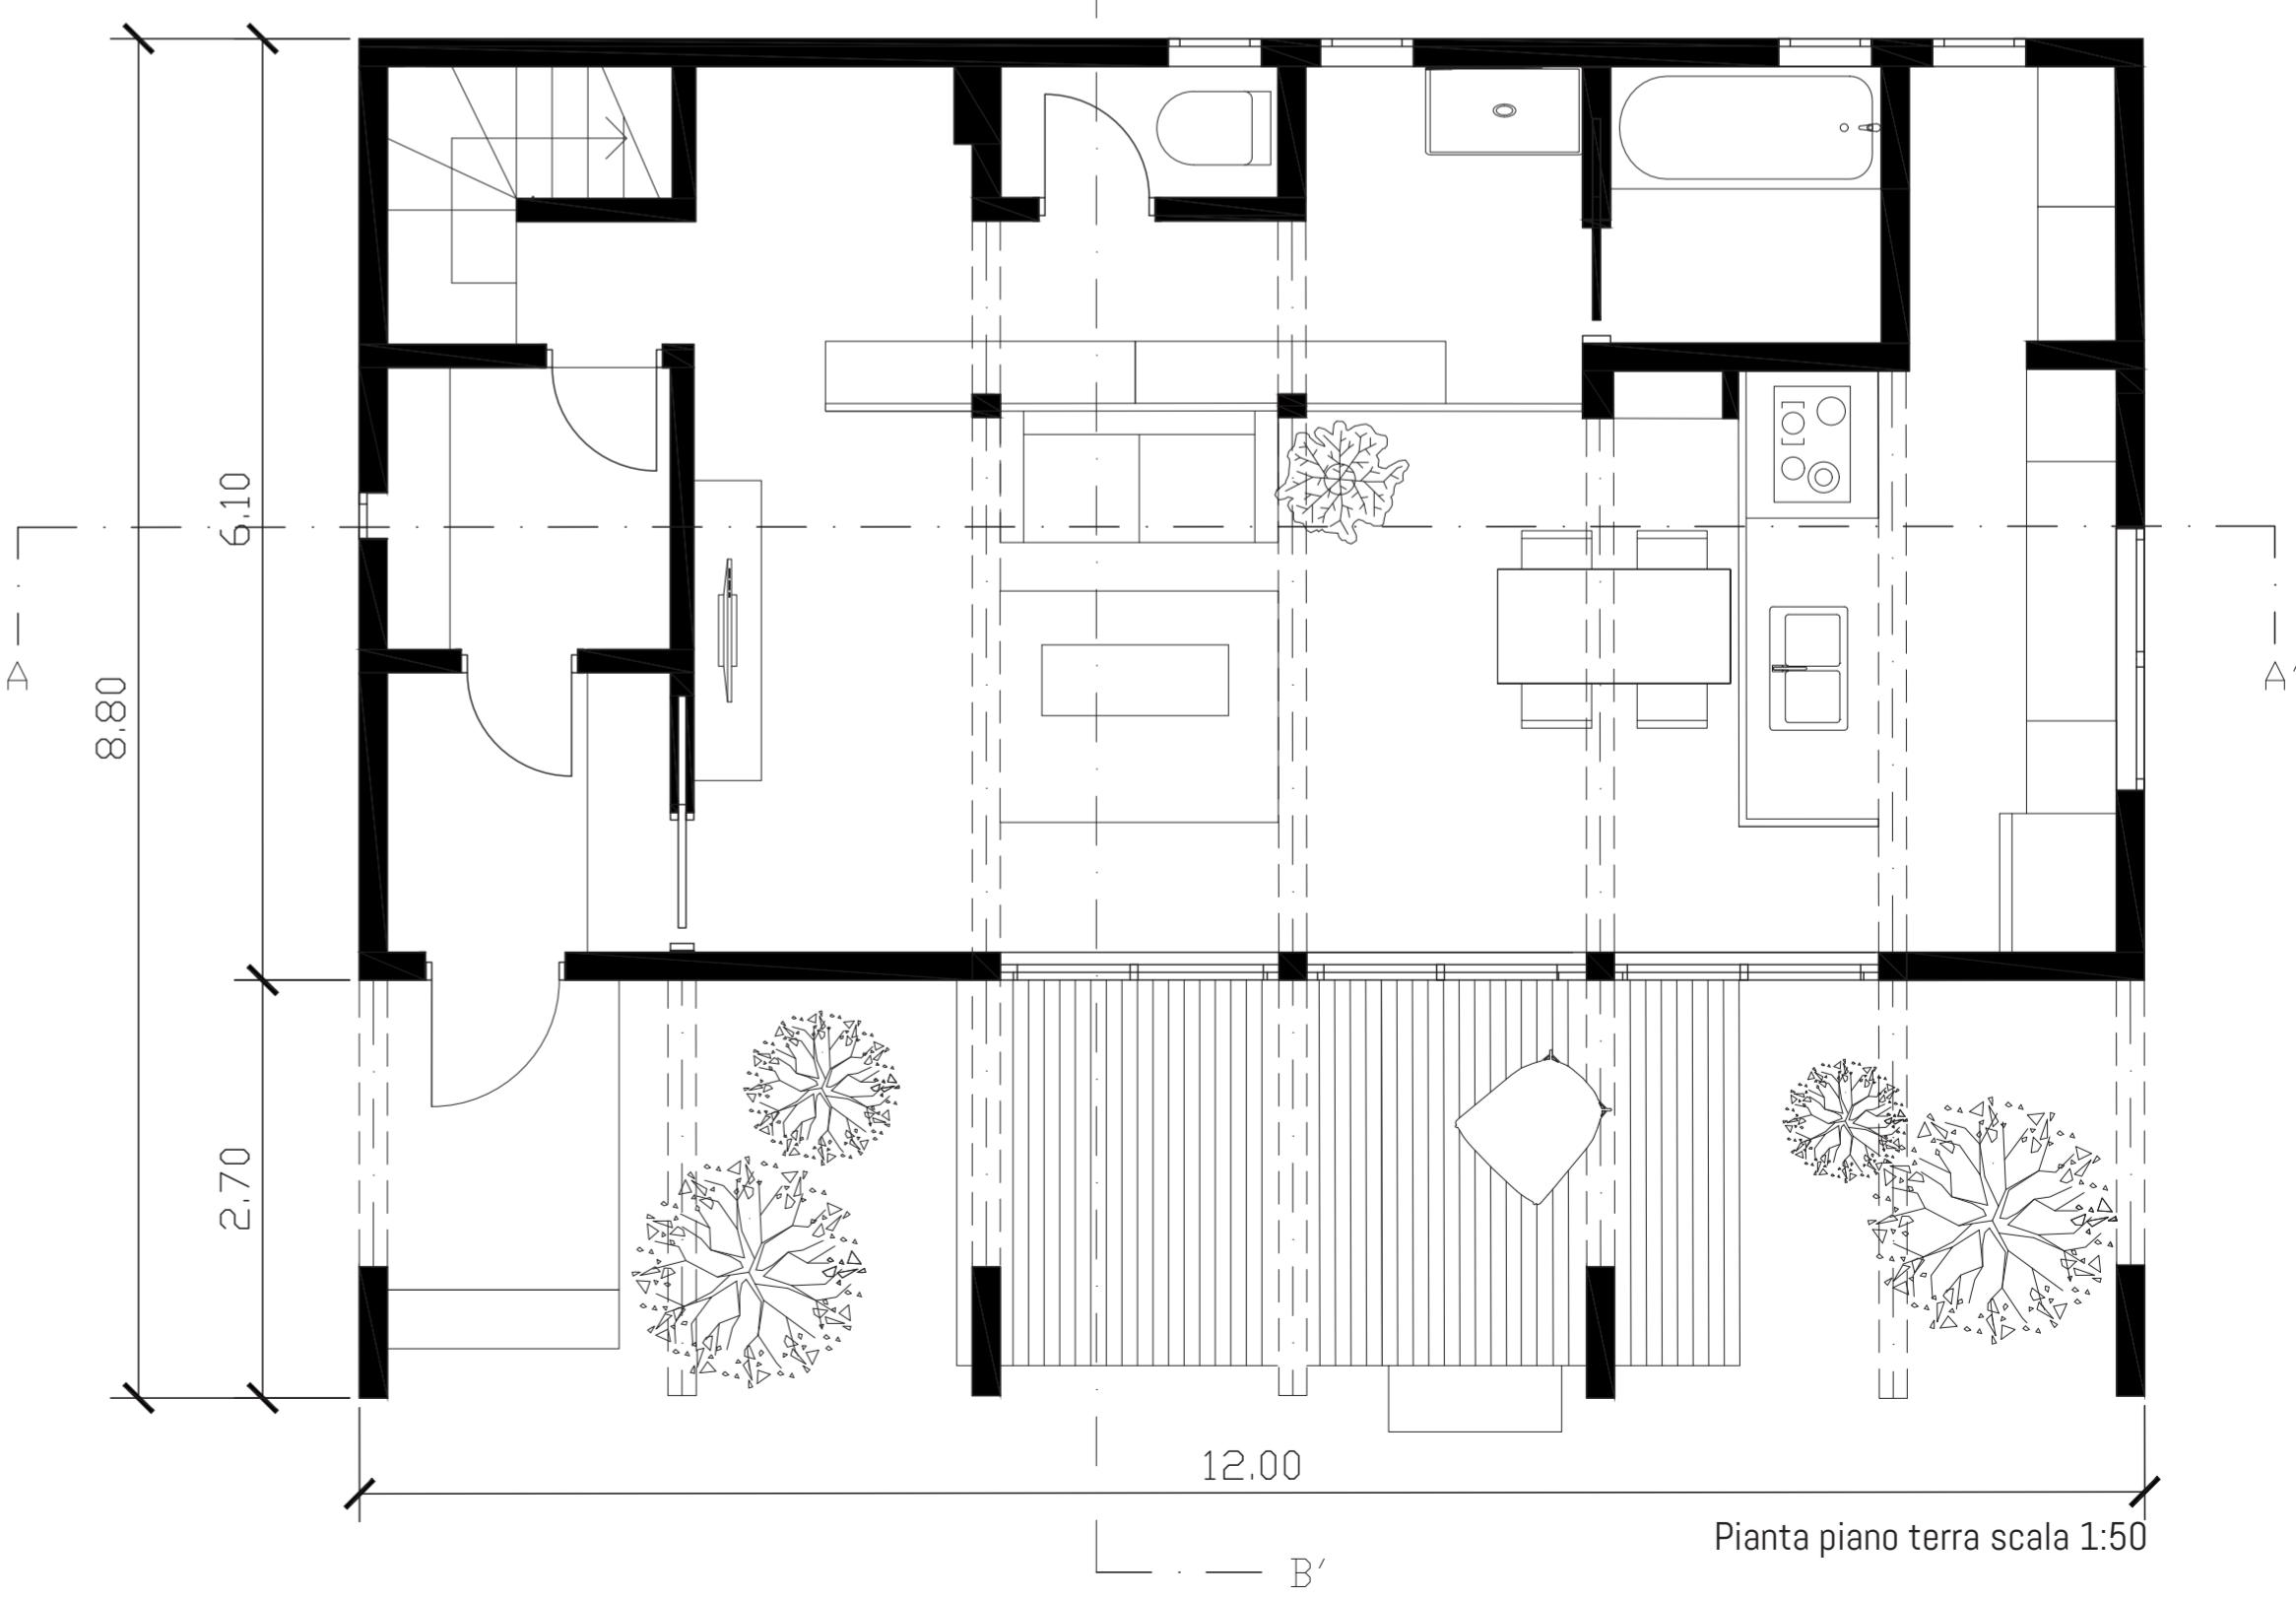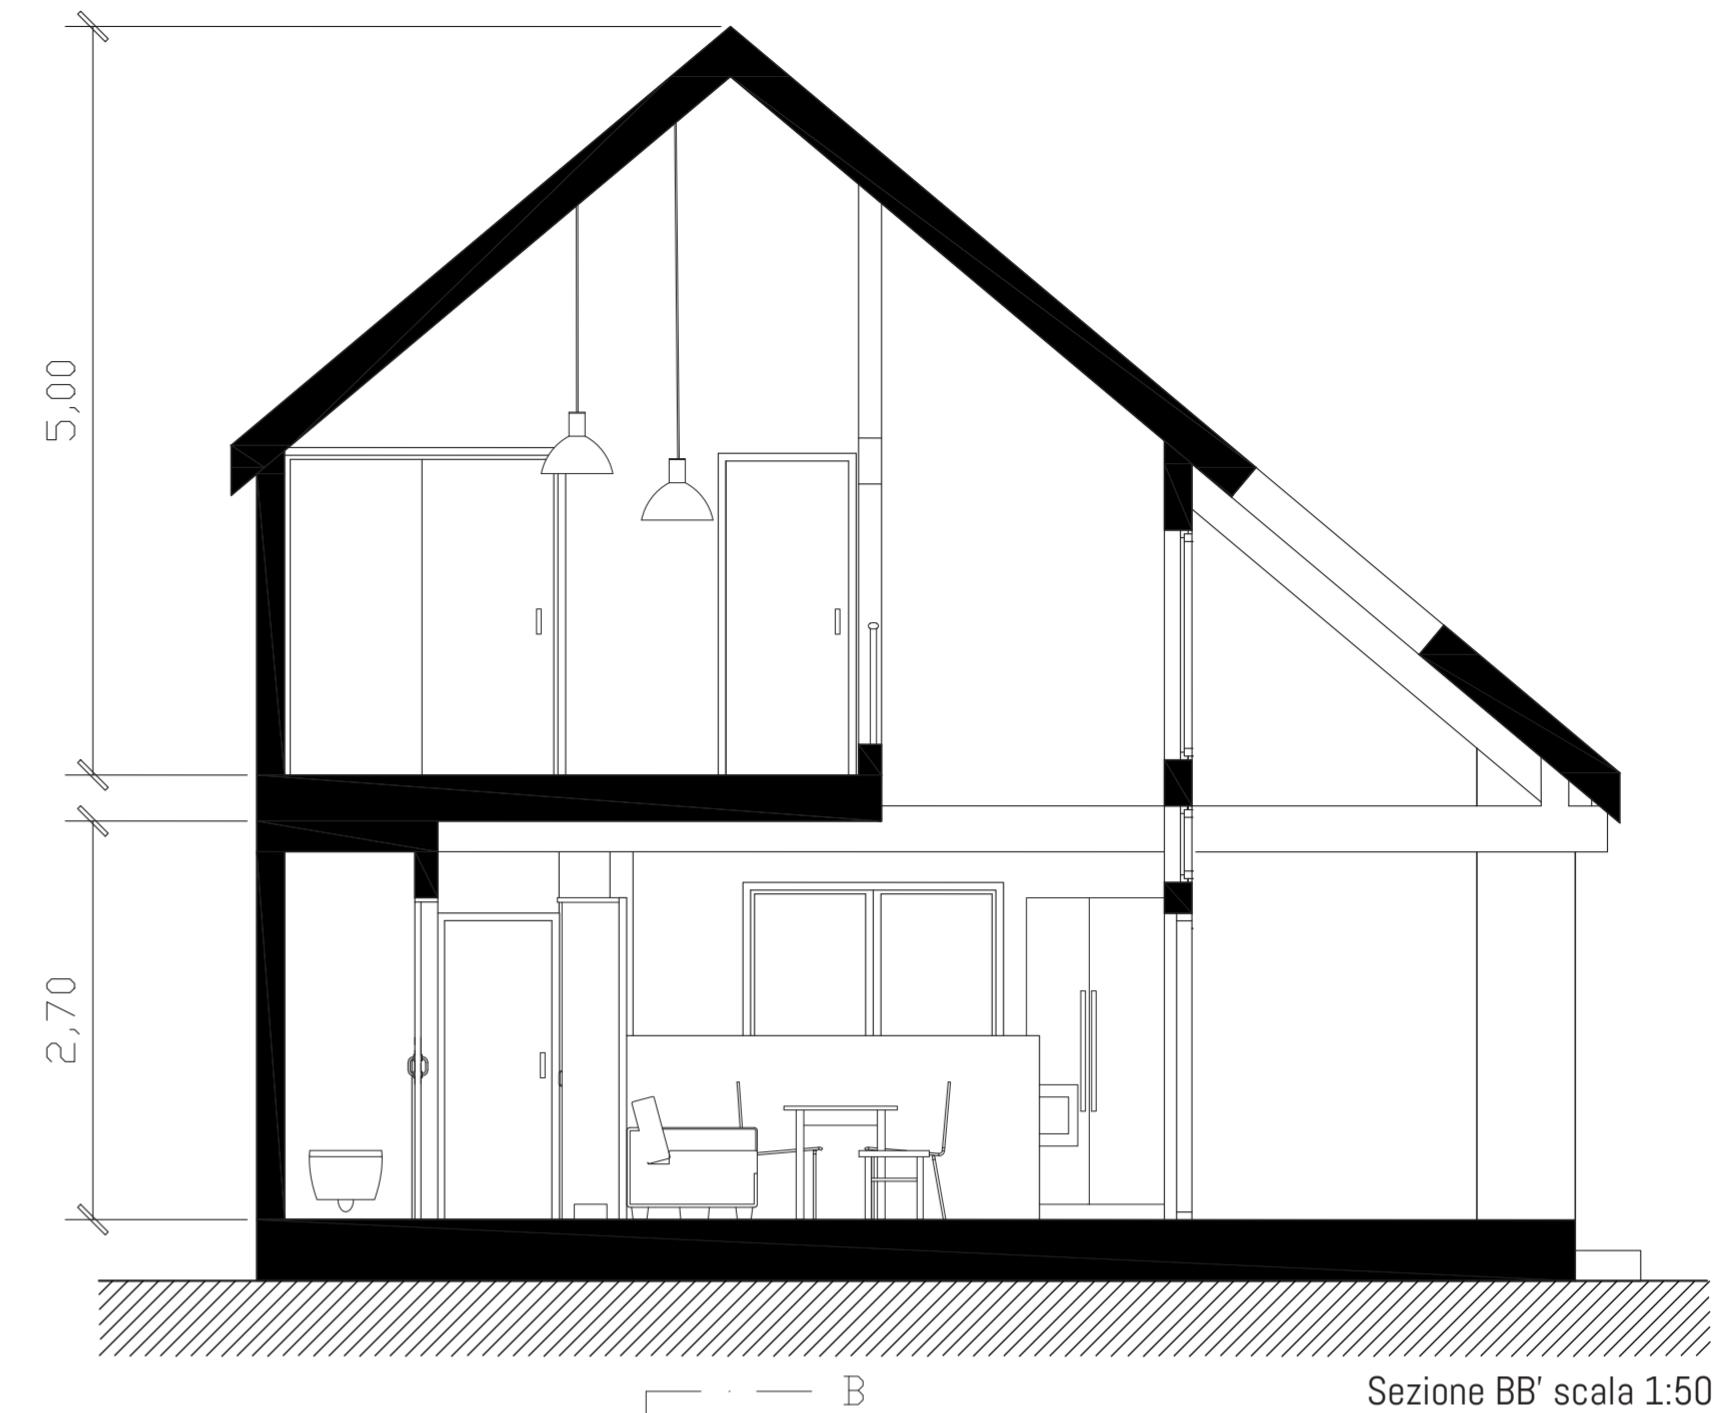

KONAN HOUSE

By ALTS Design Office

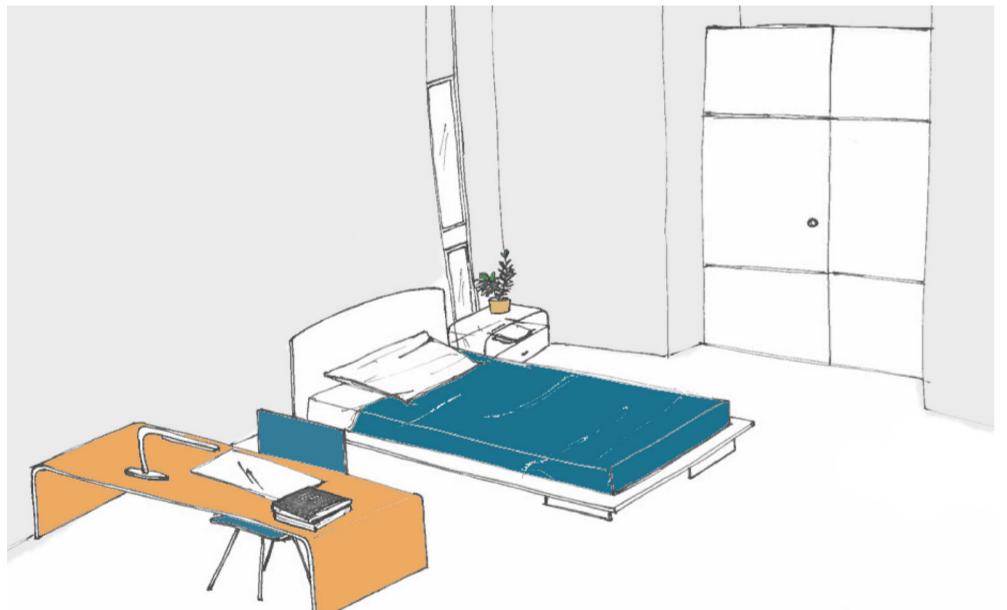

A destra: camera padronale.

All'interno letto matrimoniale, comodini moderni e la famosa Chaise Longue à réglage continu di Le Corbusier. Sul retro della piccola pianta si trova l'ingresso alla spaziosa cabina armadio.



Laboratorio di Strumenti e Metodi del Progetto
Aurora Antonini Cencicchio, Aurora Serra

