
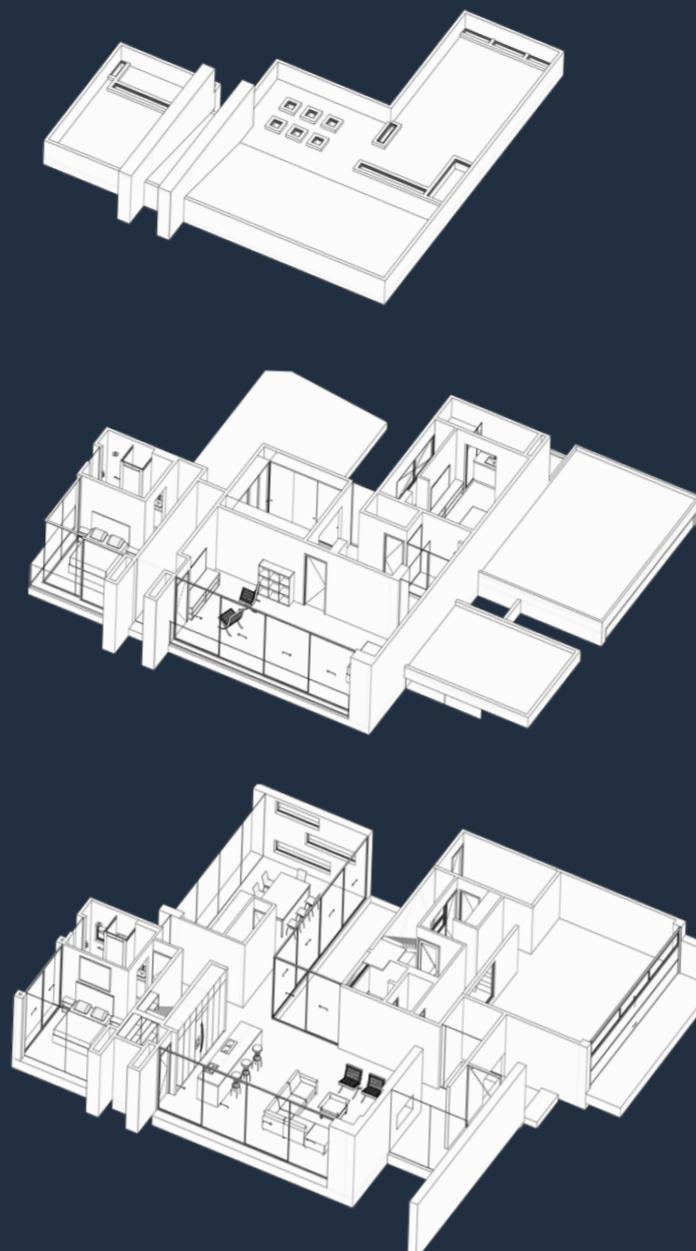


CASA CONCRETO

BY GRUPPO MM

MM Construcciones ha iniziato la sua attività nel 1988, l'azienda è stata creata con l'obiettivo di realizzare progetti, gestire e costruire opere. L'architettura di MM Construcciones è ispirata alle loro radici messicane e ha definito lo stile unico che lo identifica a prima vista.

Con l'idea di creare un'oasi in mezzo al bosco, nasce il progetto Casa Concreto. Dove il contesto della casa diventa lo scenario verde perfetto per mostrare i toni grigi del cemento che, a contatto con la natura, invecchia in modo artistico. Un accesso privato dà luogo al primo livello che, in una pianta semiaperta, si trovano le aree pubbliche. Le tre stanze sono nel secondo livello. Uno di loro ha un accesso indipendente con una scala separata.

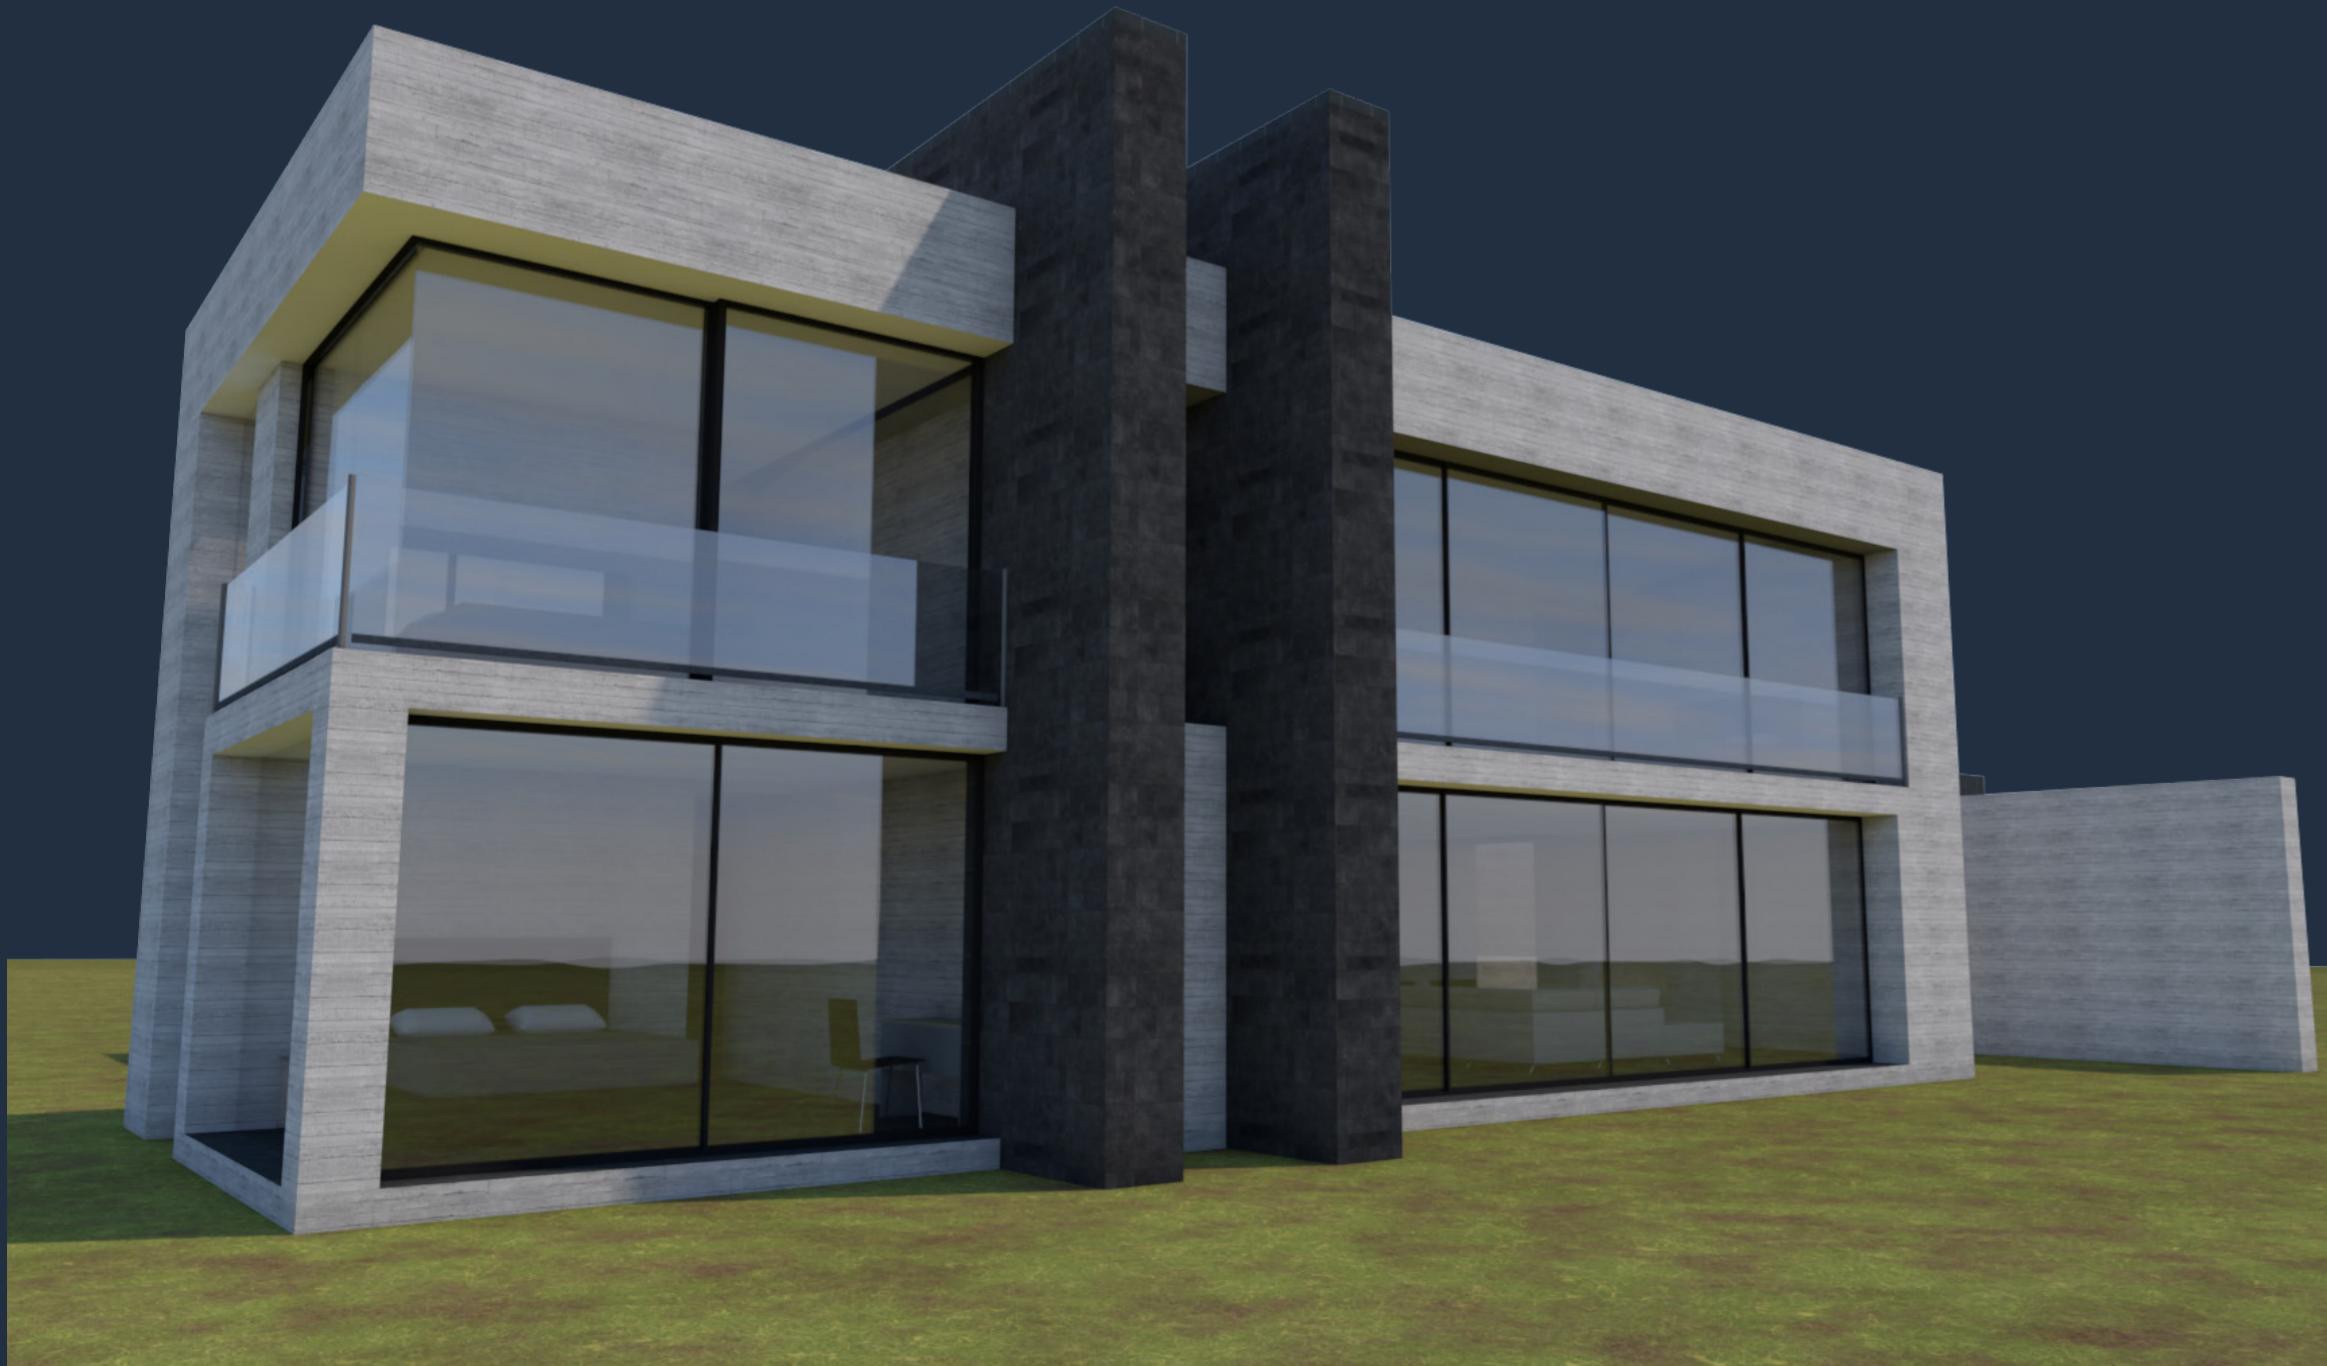





Prospetto nord Scala 1:100



La vegetazione che circonda la casa è integrata scherzosamente negli interni con patio, luce e finestre dal pavimento al soffitto. Anche le finiture e il design delle luci giocano un ruolo importante con i toni del grigio e del marrone nei pavimenti e nelle opere in legno. Questi creano un'atmosfera calda e accogliente anche con la freddezza del cemento.

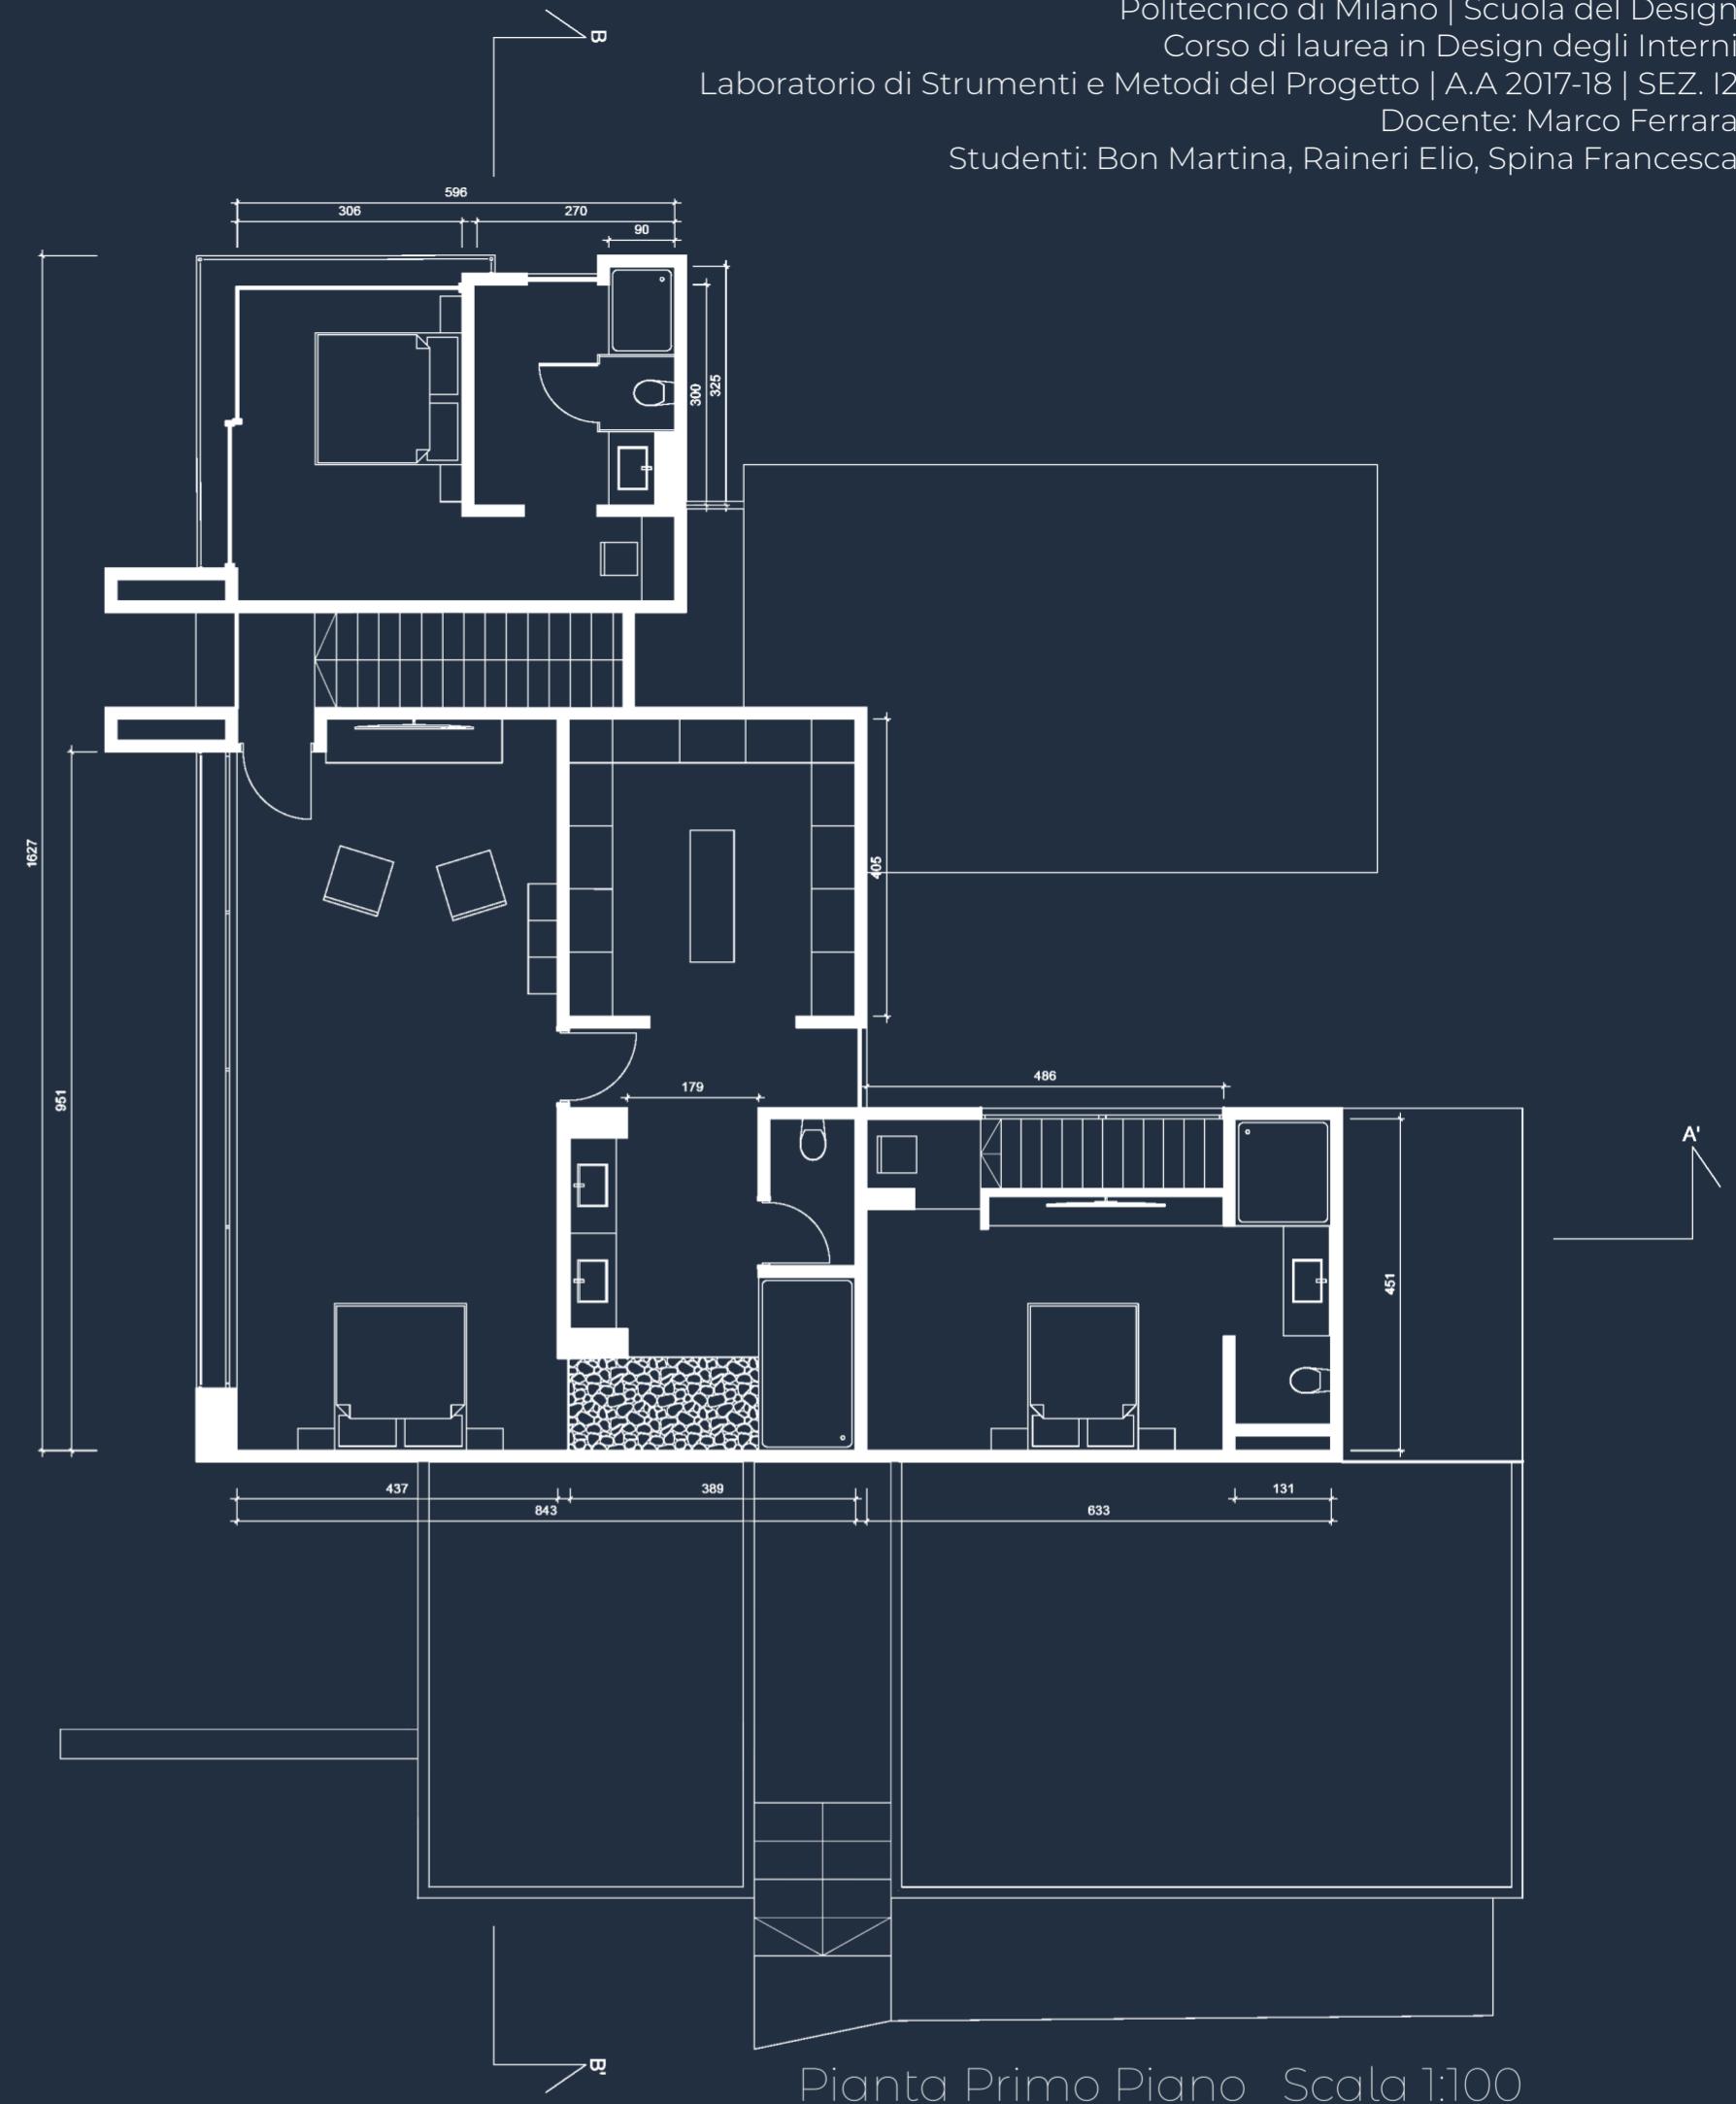

Pianta Primo Piano Scala 1:100

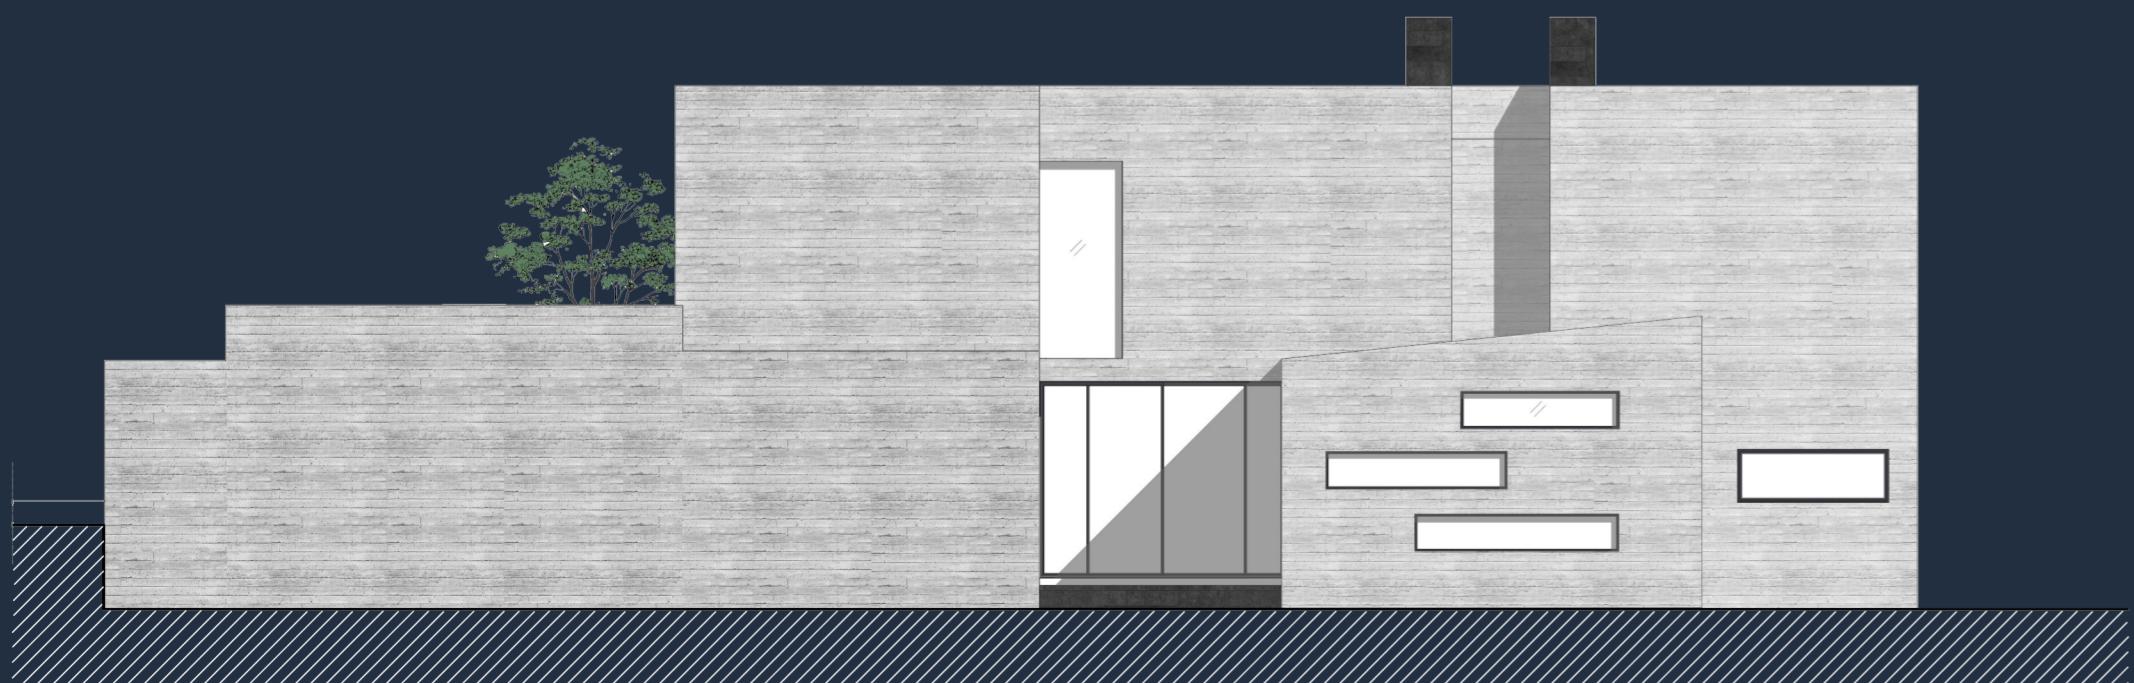

Prospetto Est Scala 1:100






Sezione BB' Scala 1:100



Prospetto Ovest Scala 1:100

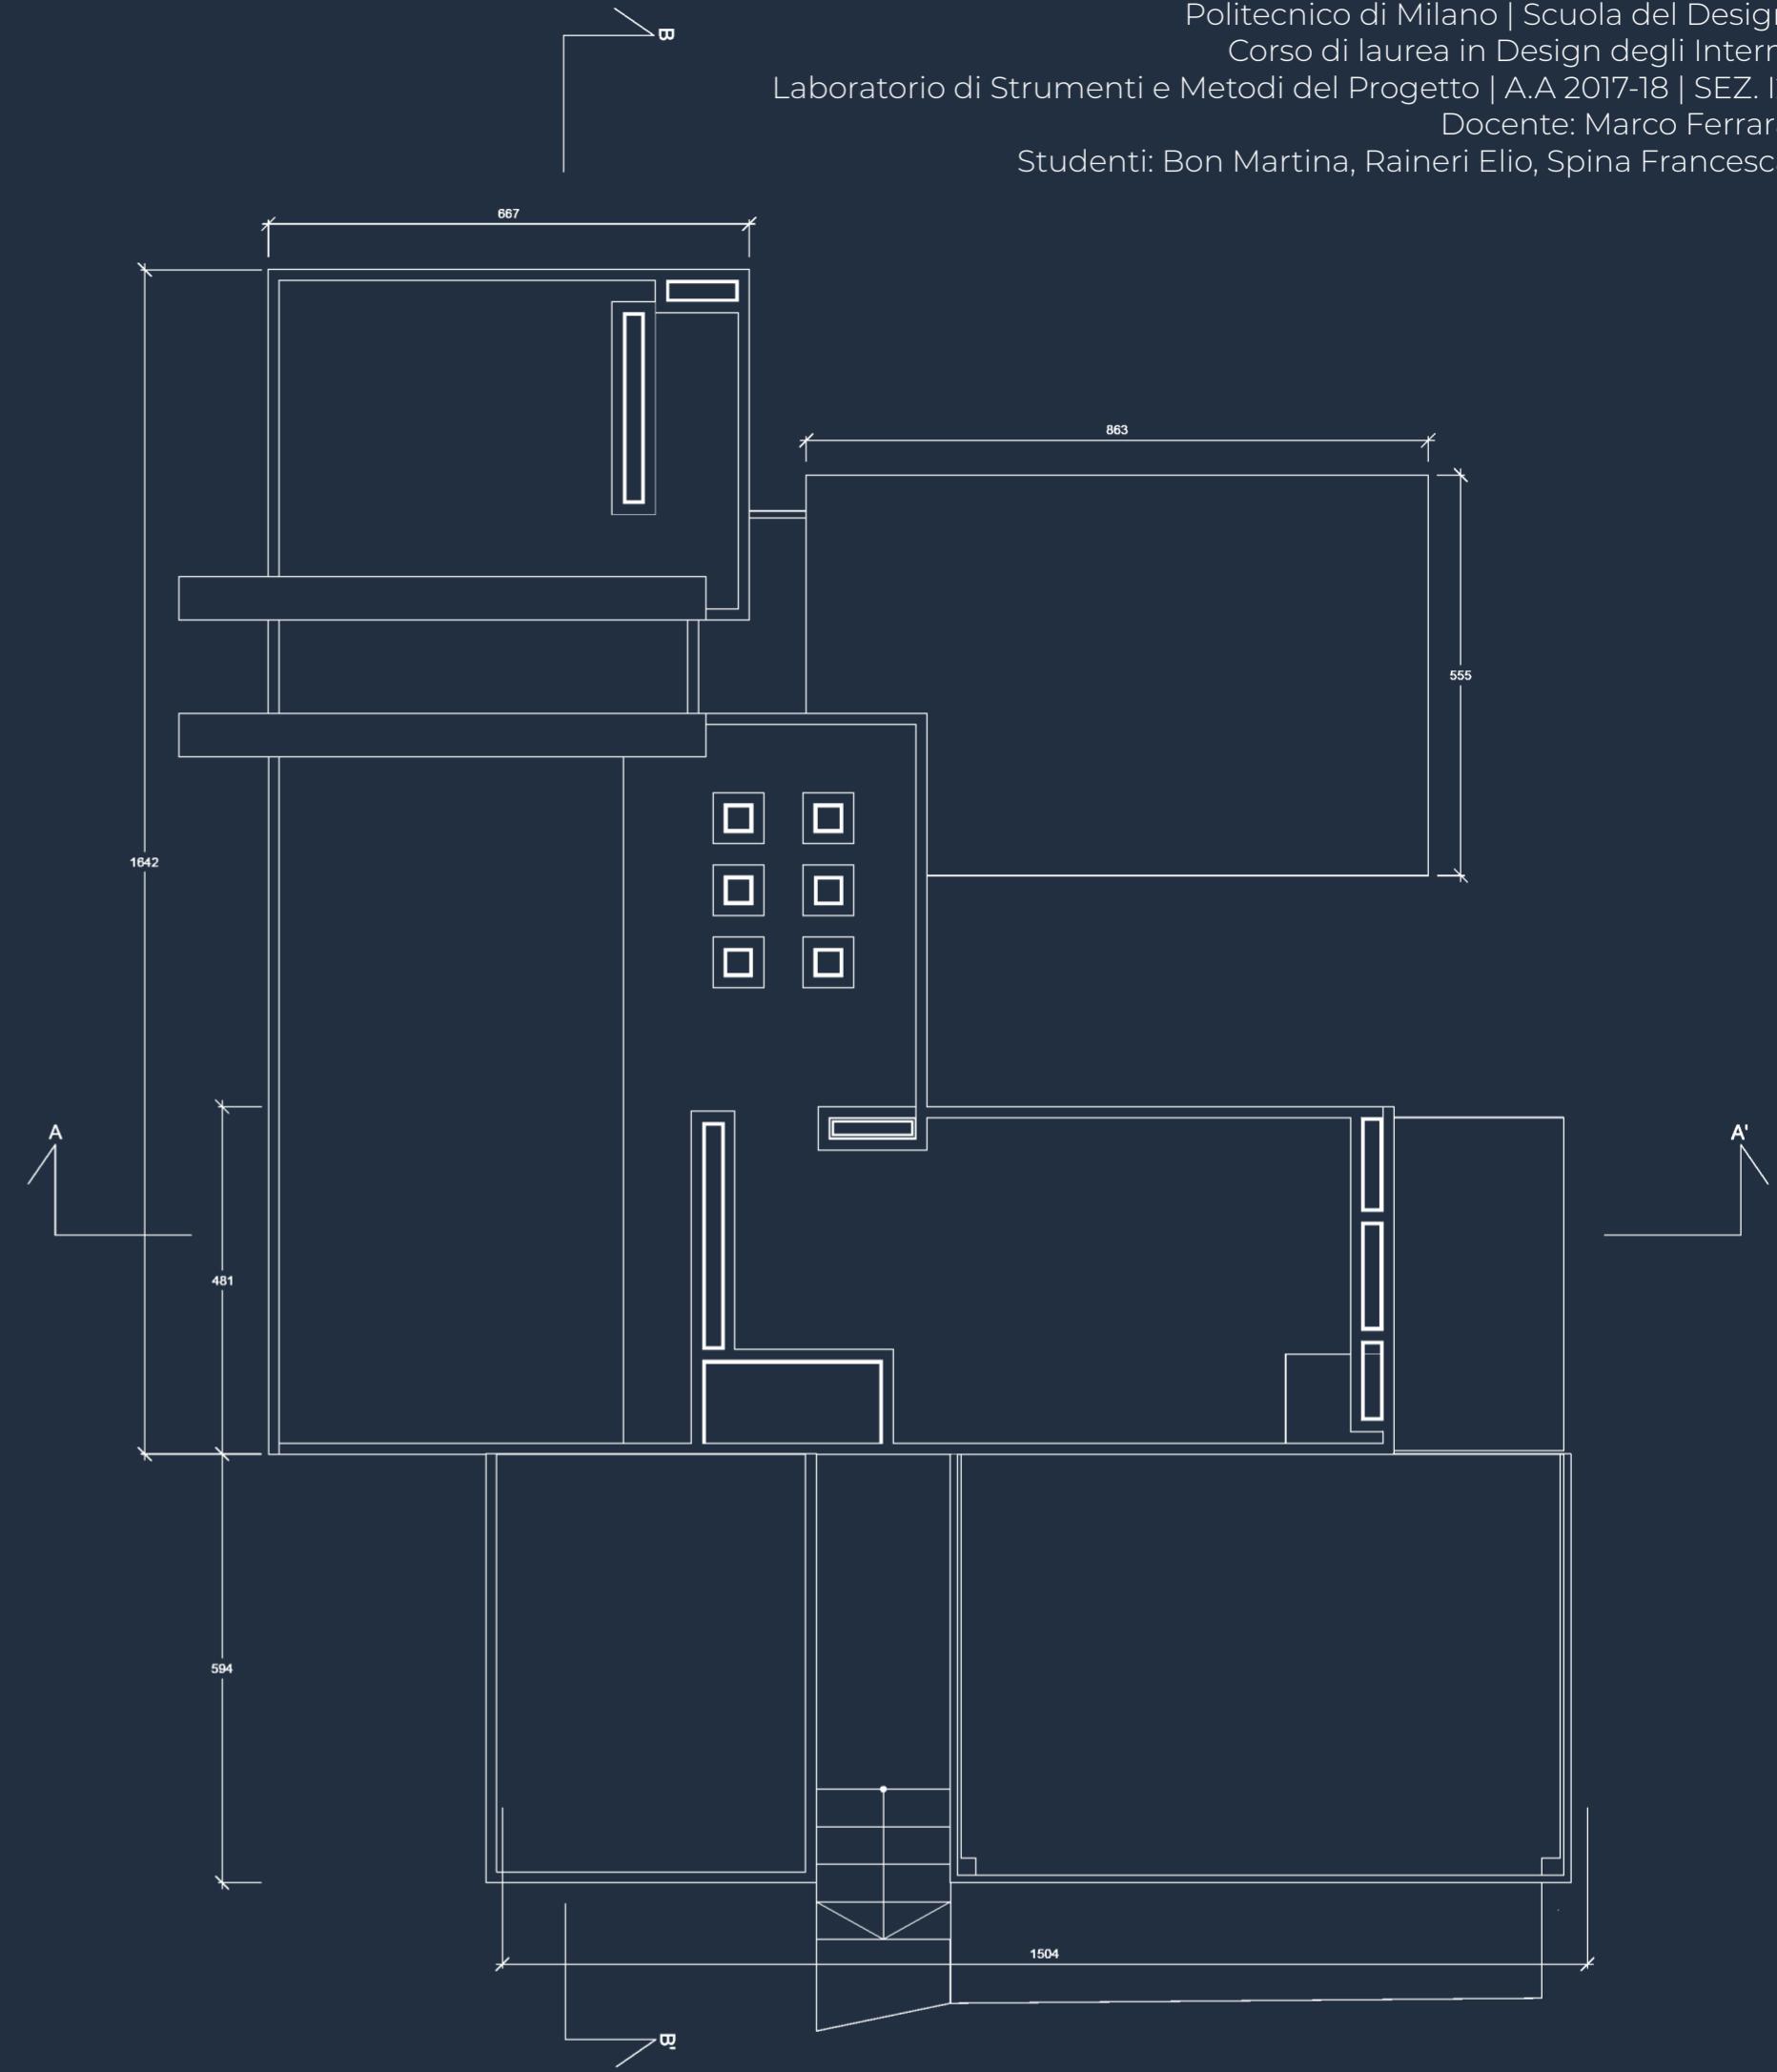

Copertura Scala 1:100



Prospetto Sud Scala 1:100