


RONDA HOUSE

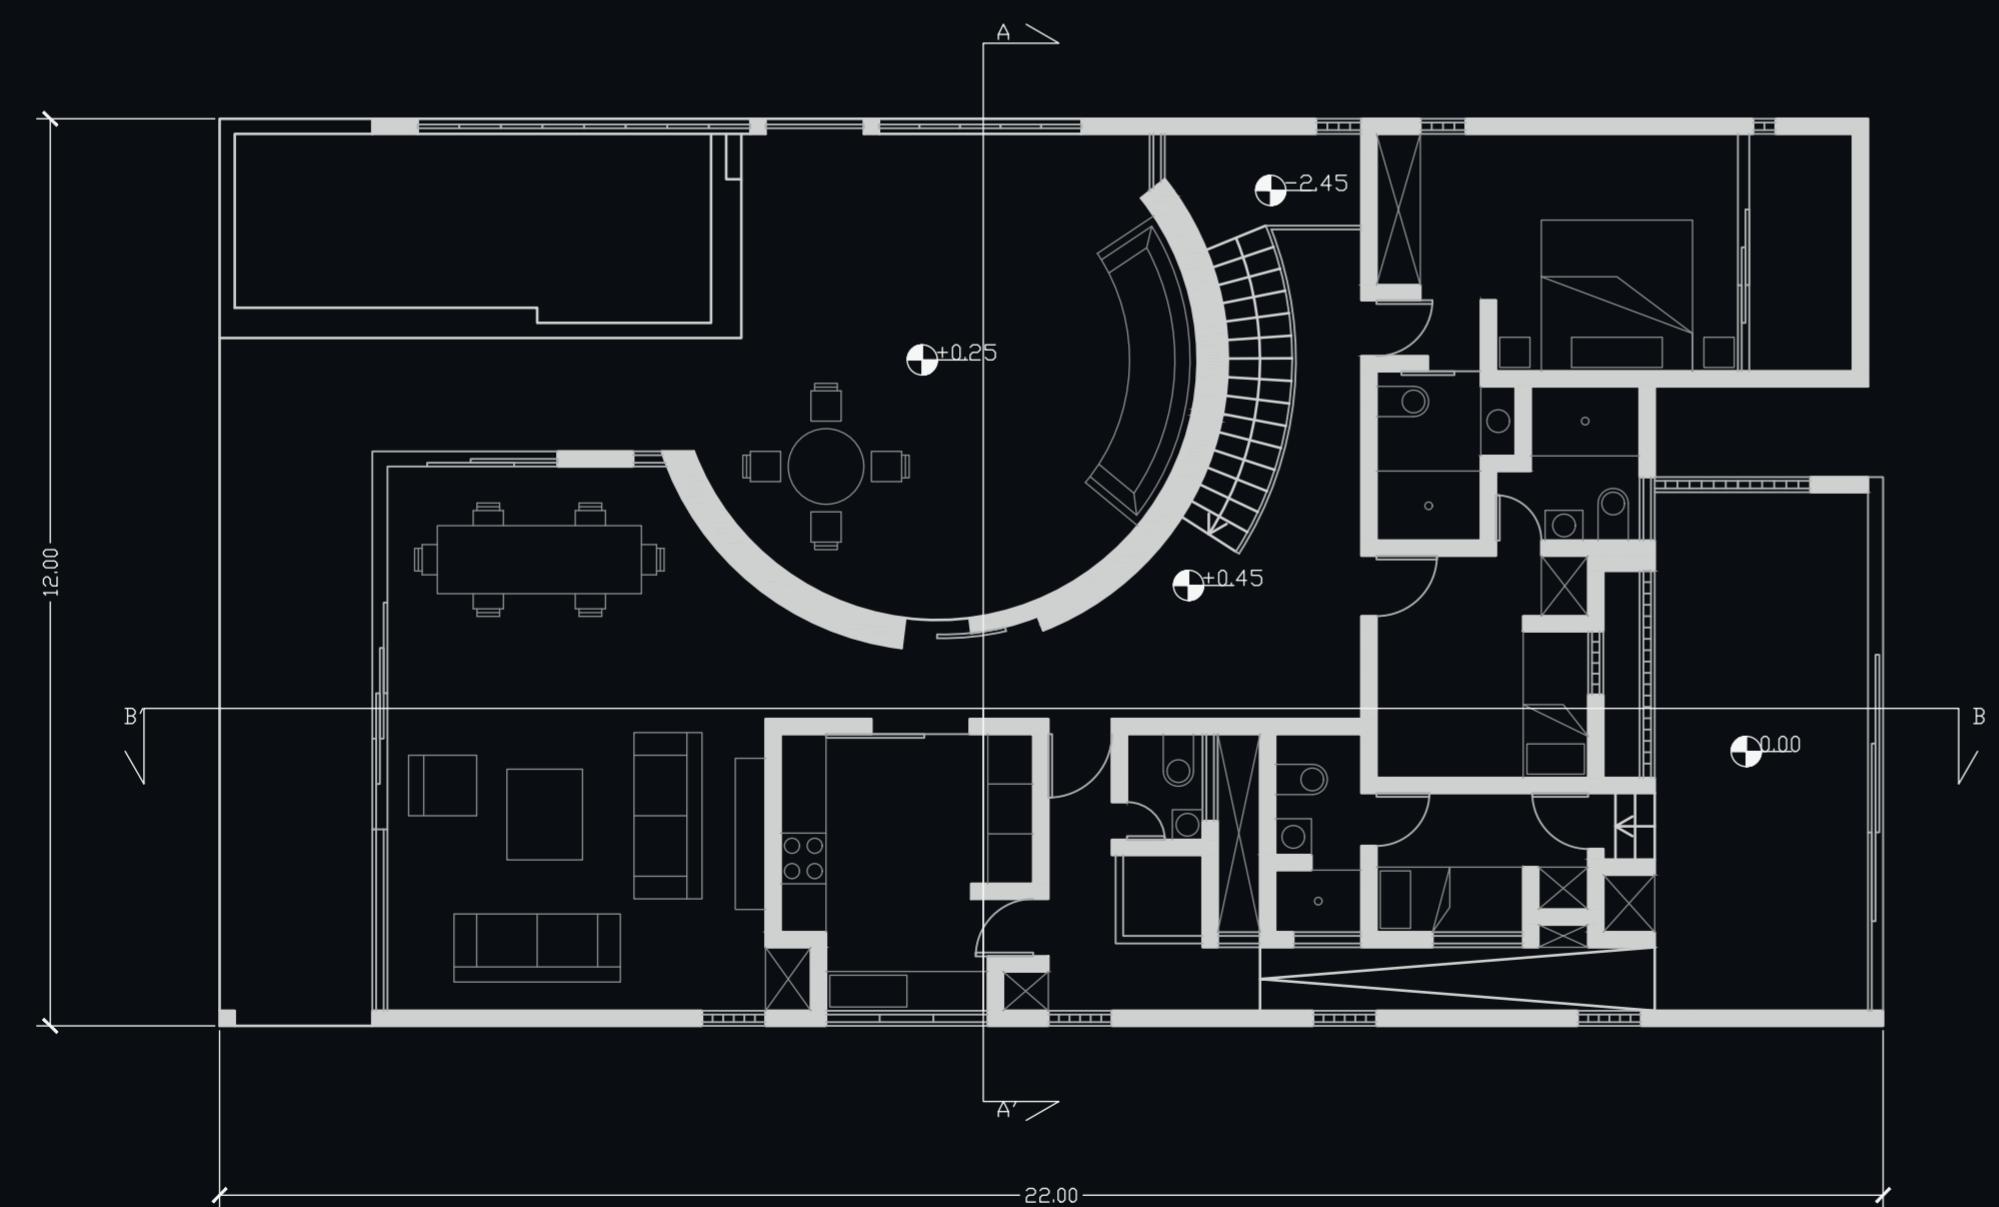

Pianta piano terra
Scala 1:100



Architetti:
Marina Vella Arquitectura Urbanismo


Località:
Distretto di Cerro Azul, Perù

Area:
362 mq



Anno di progetto:
2016

Manifattura:
Rosello

Collaborazione:
Boris Pretell, Sergio Jimenez, Cristina Tullio

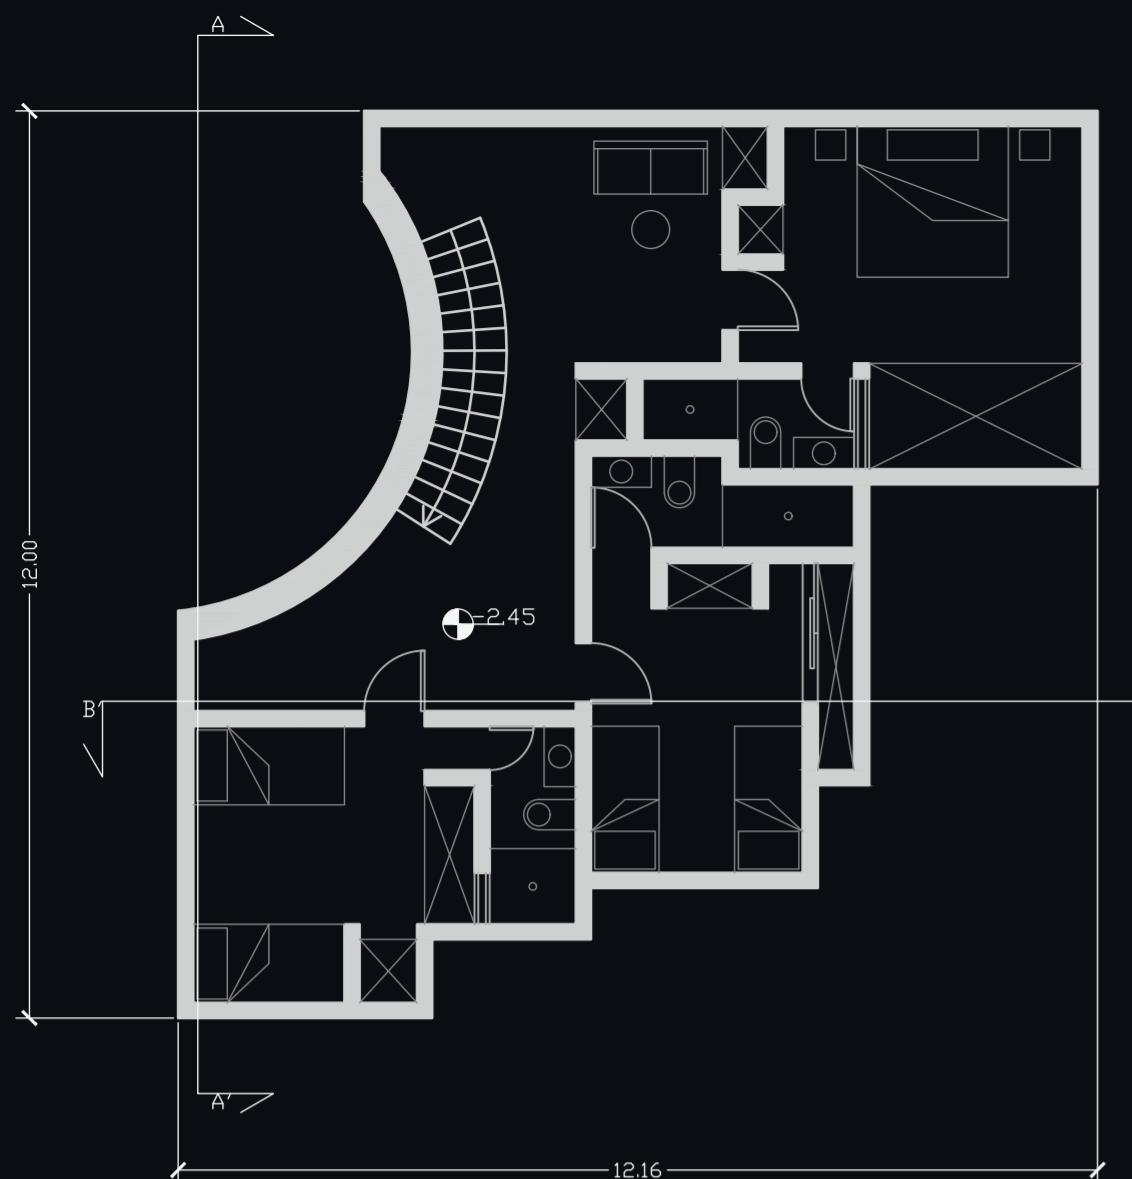

Sezione Λ-Λ'
Scala 1:100

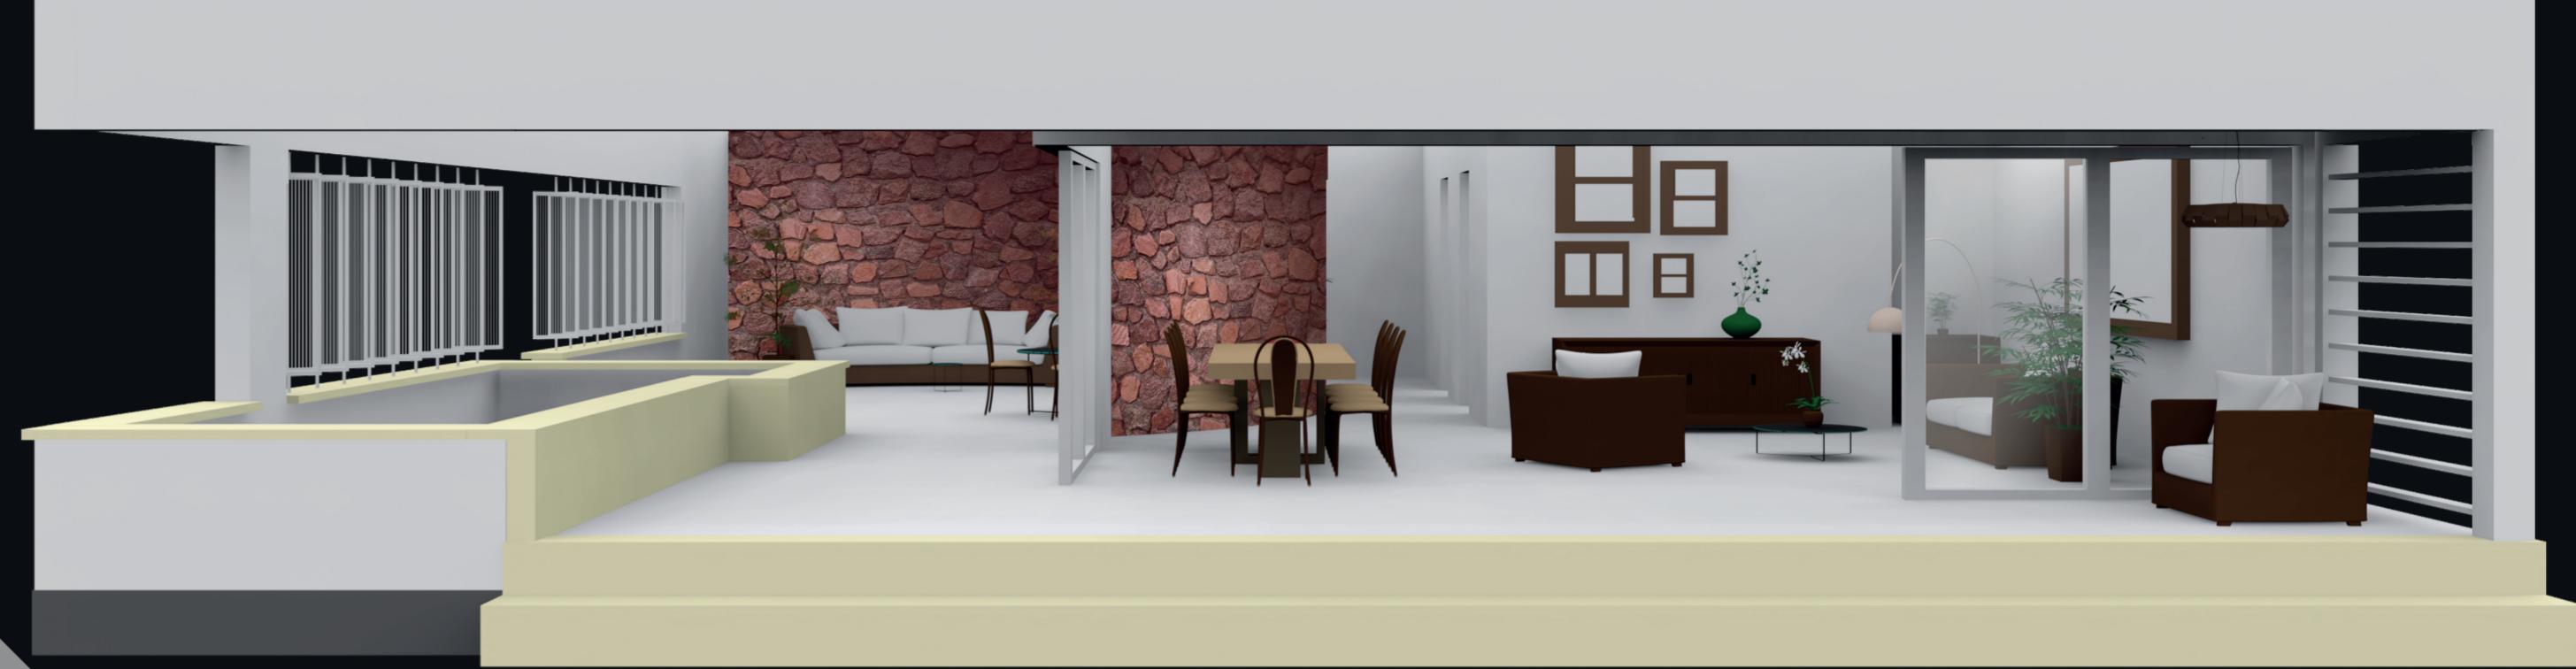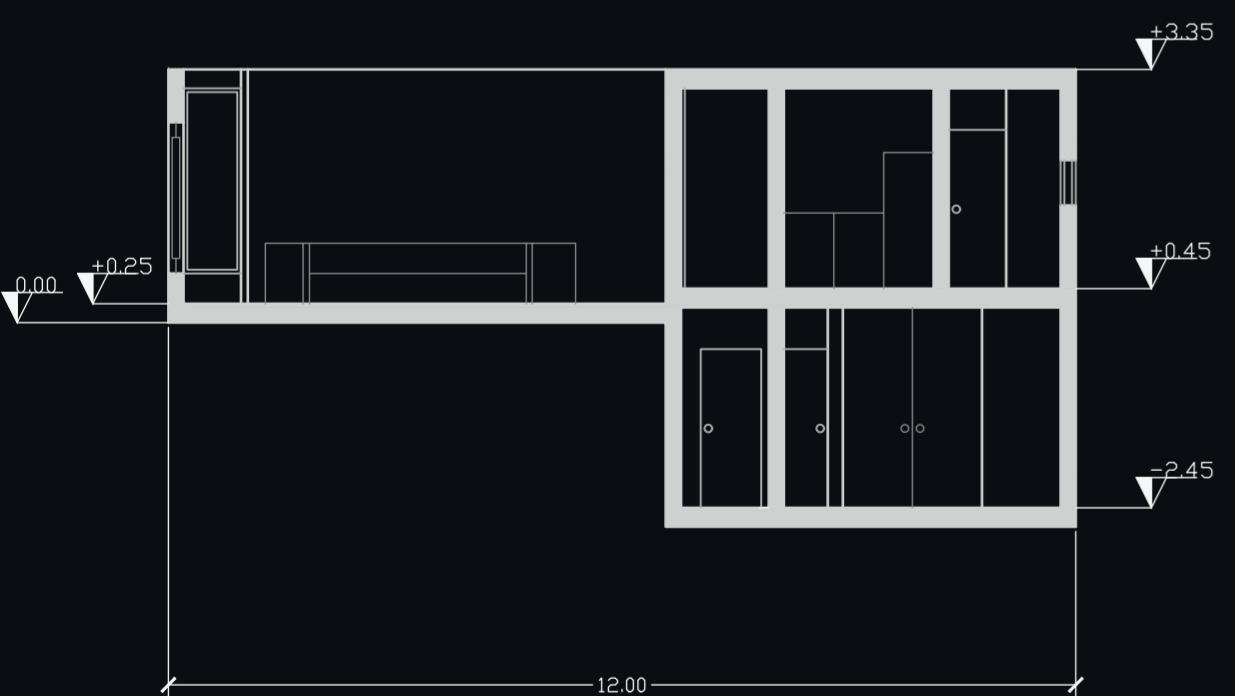

Prospecto laterale
Vista 3D



La Ronda House è costruita in un sito privilegiato su un lotto rettangolare che misura 12 metri di lunghezza e 22 metri di larghezza.

Si affaccia sull'Oceano Pacifico, e ha una vista laterale di sabbie bianche e dune, ed è coperta alle spalle da una bellissima collina rossa, da cui il nome del luogo: Cerro Colorado.

Rigide e rigorose regolamentazioni di costruzione che specificavano altezze, materiali, includendo tinte di bianco, ecc., dovevano essere trattate affinchè seguissero sé stesse e le aspettative personali della famiglia, che sognò di un'architettura organica con accoglienti aree di raccolta riparate dalle giornate ventose.

Il progetto incoraggia una continua connessione con l'ambiente circostante tramite uno spazio esterno con partizioni aperte sul mare, espandendo gli interni e permettendo la permeazione degli esterni, mentre le vite degli inquilini ruotano attorno la terrazza centrale, evidenziata da uno spesso muro semicircolare in pietra rossa originaria della vicina collina.

Il colore rosso della pietra naturale usato nella terrazza forma un contrasto con la tinta bianco puro di questa casa su due livelli.

Usando questa ruvida pietra rossa naturale, e posizionandola al centro della casa, le rigorose regolamentazioni di costruzione sono adempiute, inglobando gli spazi in colore e forma per le attività della famiglia e amici grazie al bianco lineare della casa e all'organico muro semicircolare, e diventando visivamente parte delle Red Hill e una protezione dalle giornate ventose.

Arearie di circolazione, scale e corridoi alle camere da letto sono organizzati attorno al muro semicircolare in pietra.

Luce e ventilazione naturale sono assicurate dal cielo e dalle piccole terrazze, che riempiono le camere da letto e le aree circostanti con luce, e infondono la casa con l'atmosfera allegra di una vacanza al mare.



Sezione B-B'
Scala 1:100

