


# COURTYARD HOUSE

## by INOSTUDIO

POLITECNICO DI MILANO  
 LABORATORIO DI STRUMENTI E METODI DEL PROGETTO  
 DESIGN DEGLI INTERNI - I2  
 ANDREA ATZENI  
 ELEONORA PROSERPIO  
 LORENZO BUGA

La casa si trova vicino alla foresta, in una zona densa di abitazioni mono-familiari. La location e la vicinanza con il bosco sono alla base dei concetti che fondono il progetto di INOSTUDIO per quanto riguarda la forma e struttura della villa. Il piano terra si estranea dalla presenza dei vicini grazie all'assenza di finestre nei muri laterali, rimanendo aperta verso il giardino e sul cortile. Le terrazze del piano superiore sono spazi esterni intimi all'interno alla casa. Essa da la possibilità di avere una vista sul paesaggio e vivere l'atmosfera del luogo. Grazie alle aperture e alla serra la natura viene integrata all'interno dello spazio domestico.

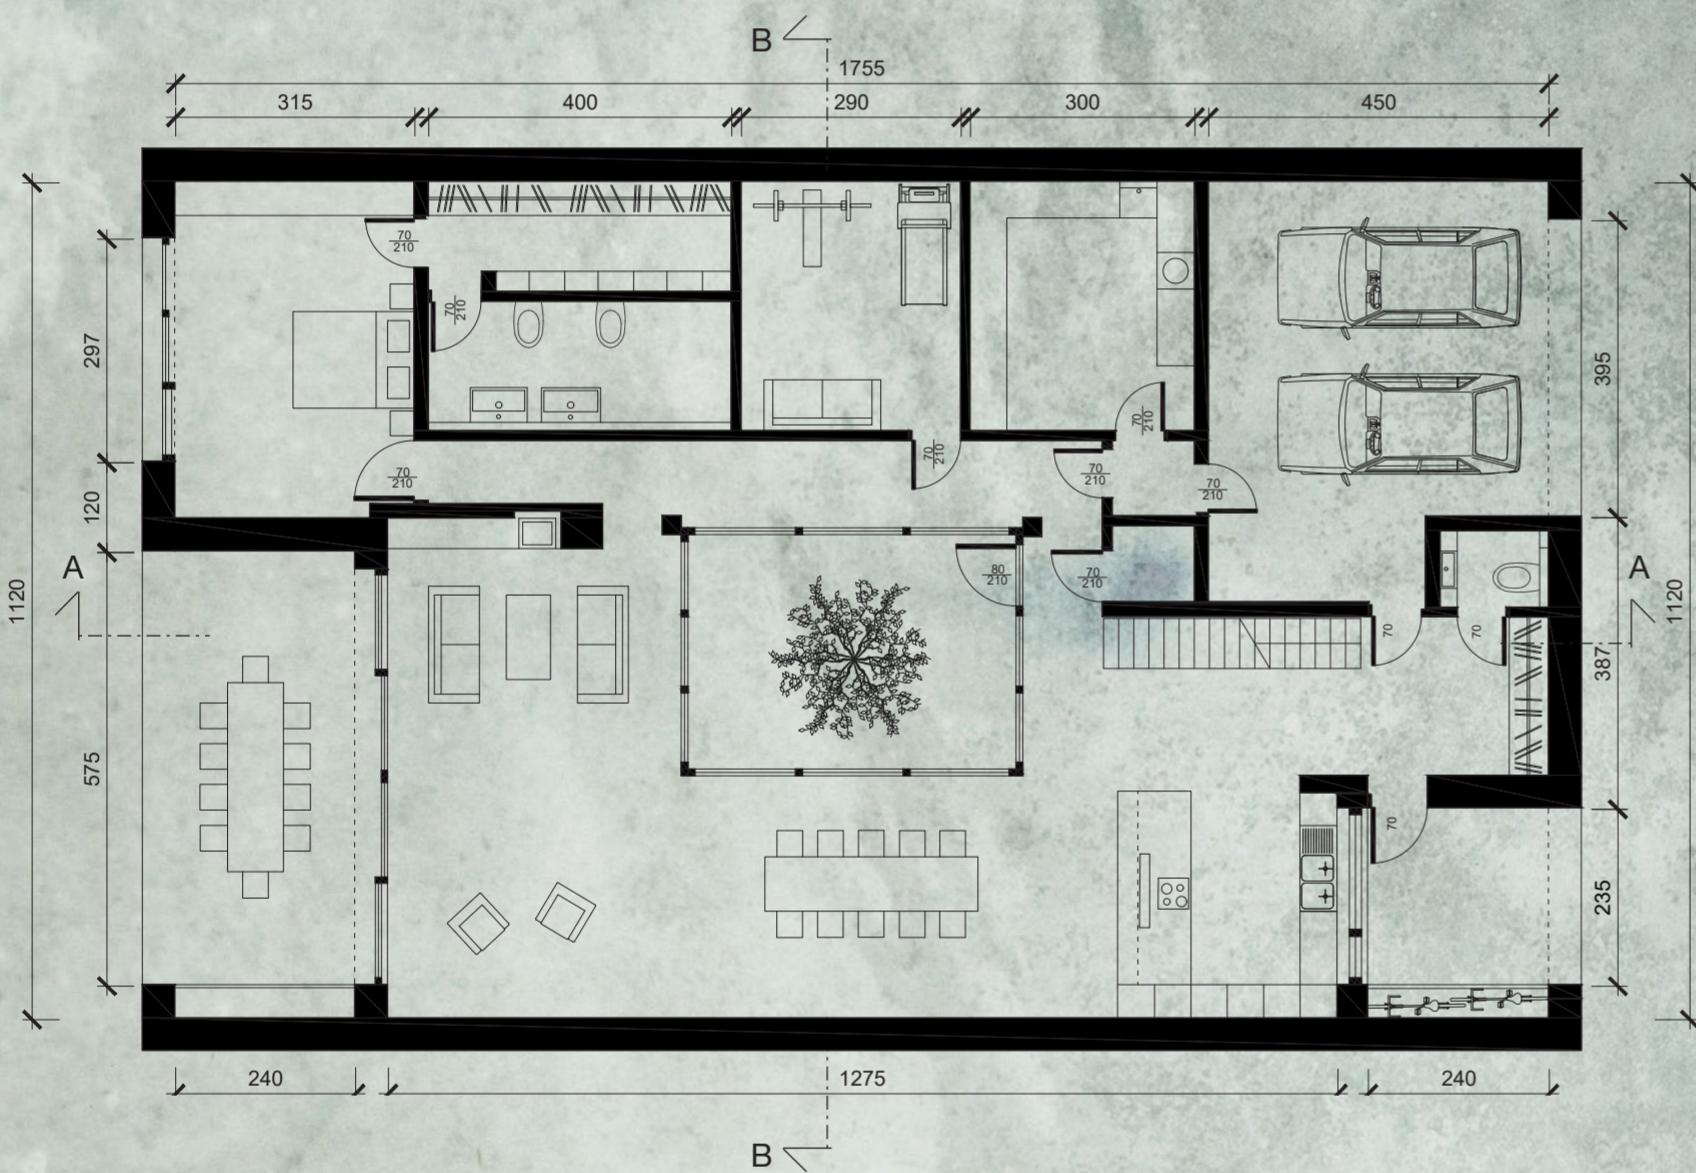


Pianta piano terra scala 1:100


Esploso assonometrico




Sintesi della relazione della casa con l'albero

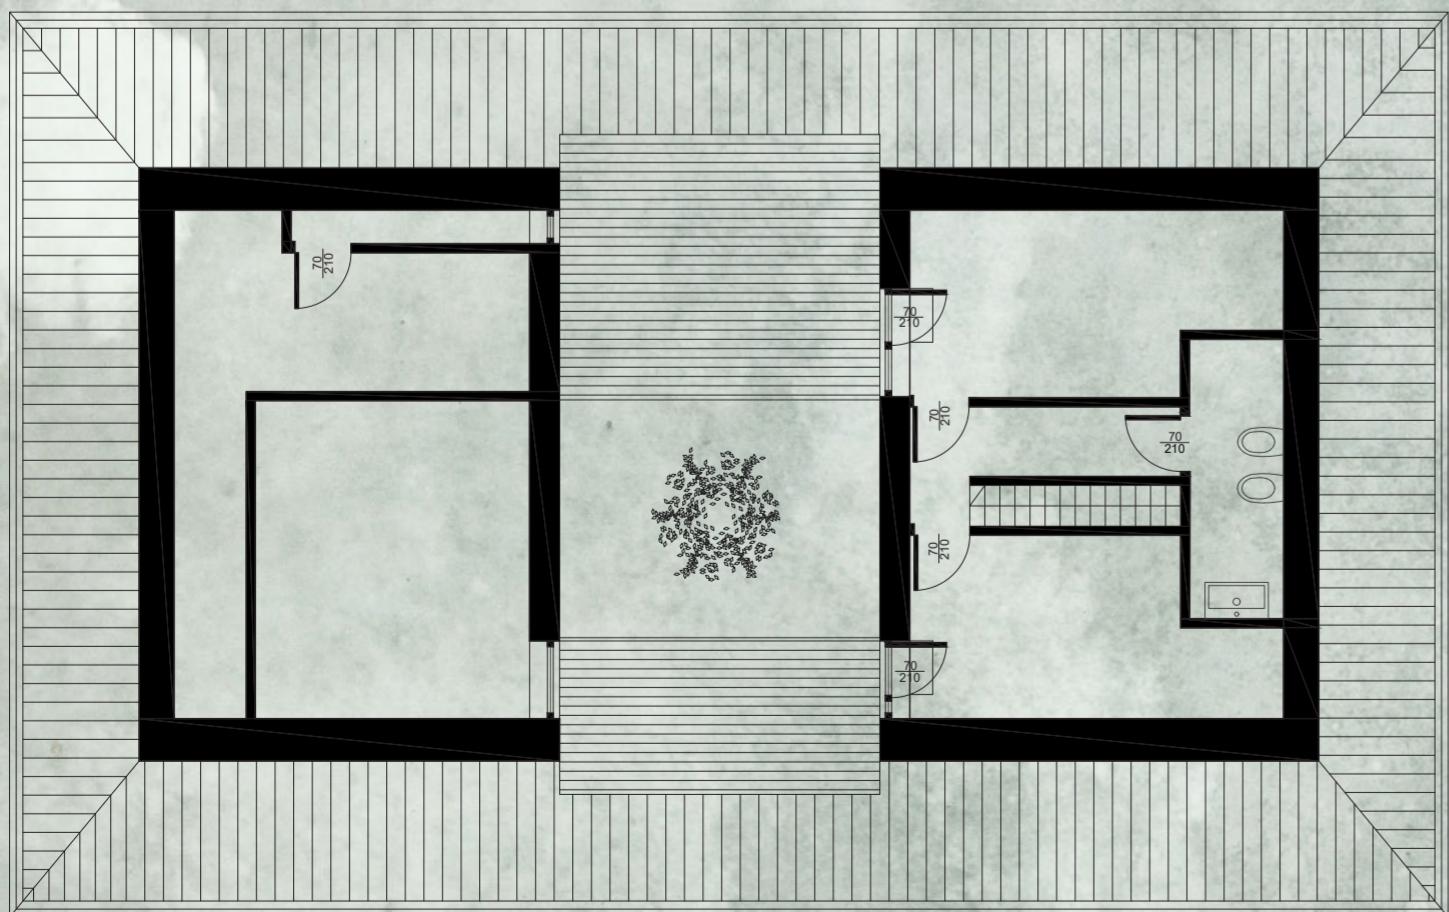


Pianta piano primo scala 1:100

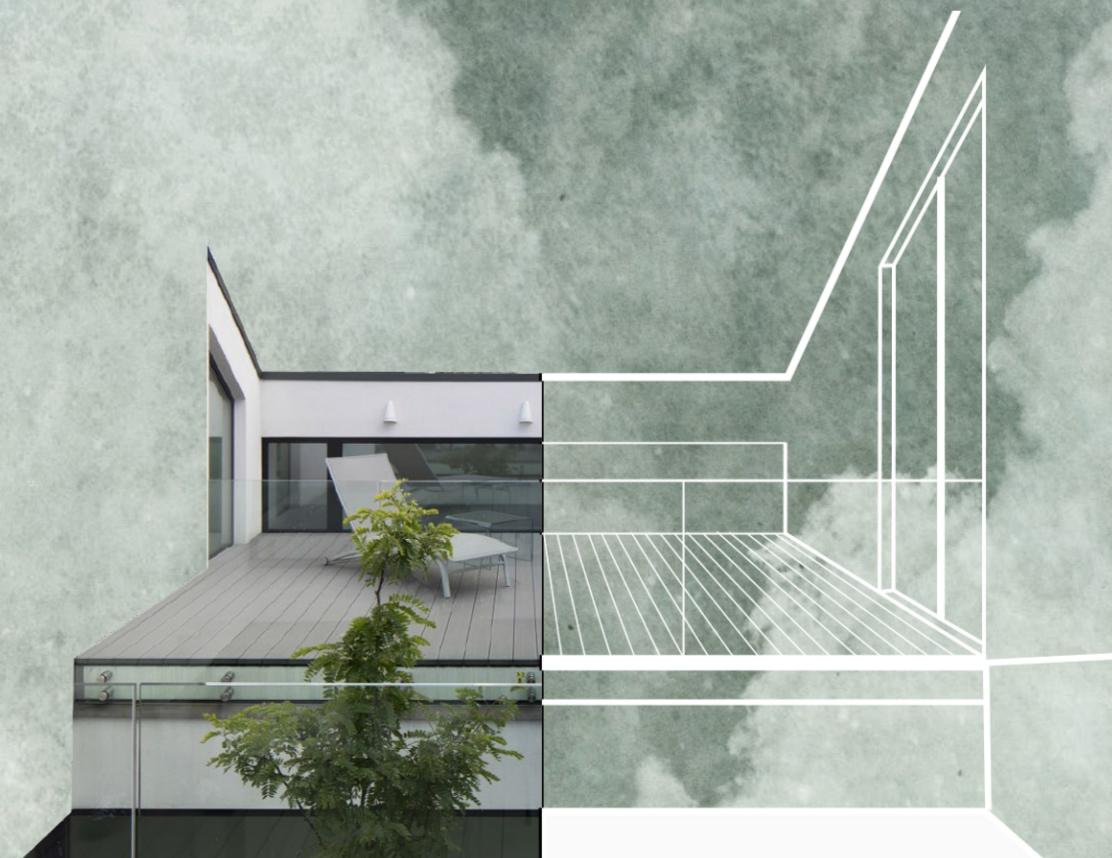


Vista del terrazzo

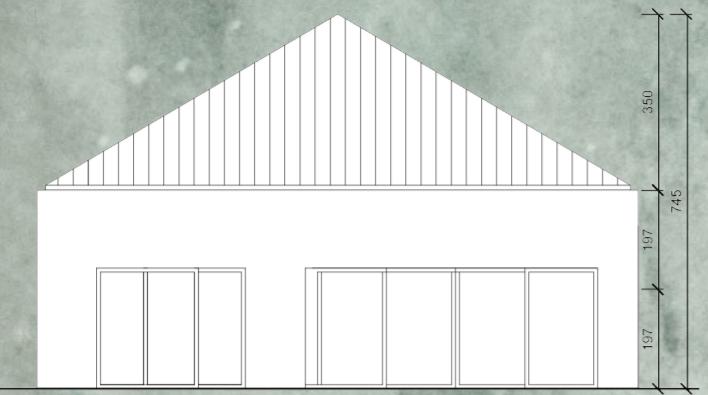


Prospetto est scala 1:200

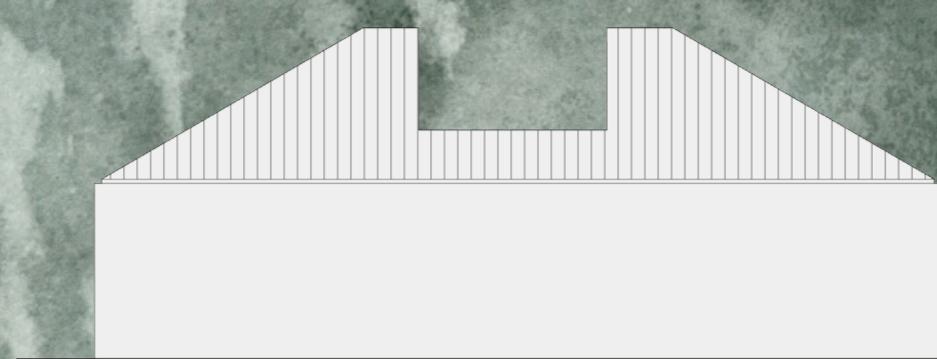


Prospetto nord-sud scala 1:200

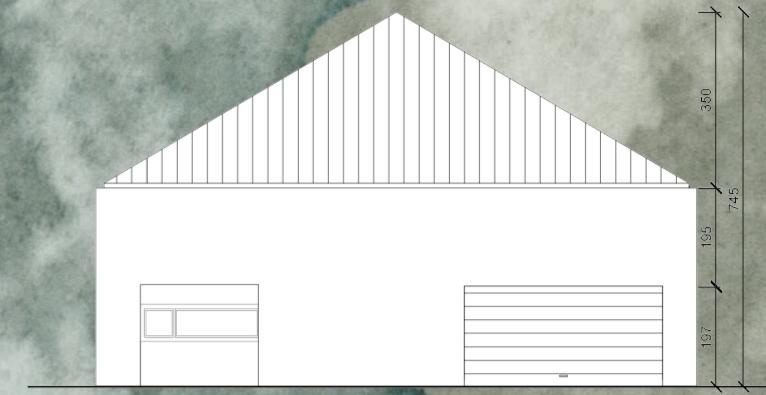


Prospetto ovest scala 1:200

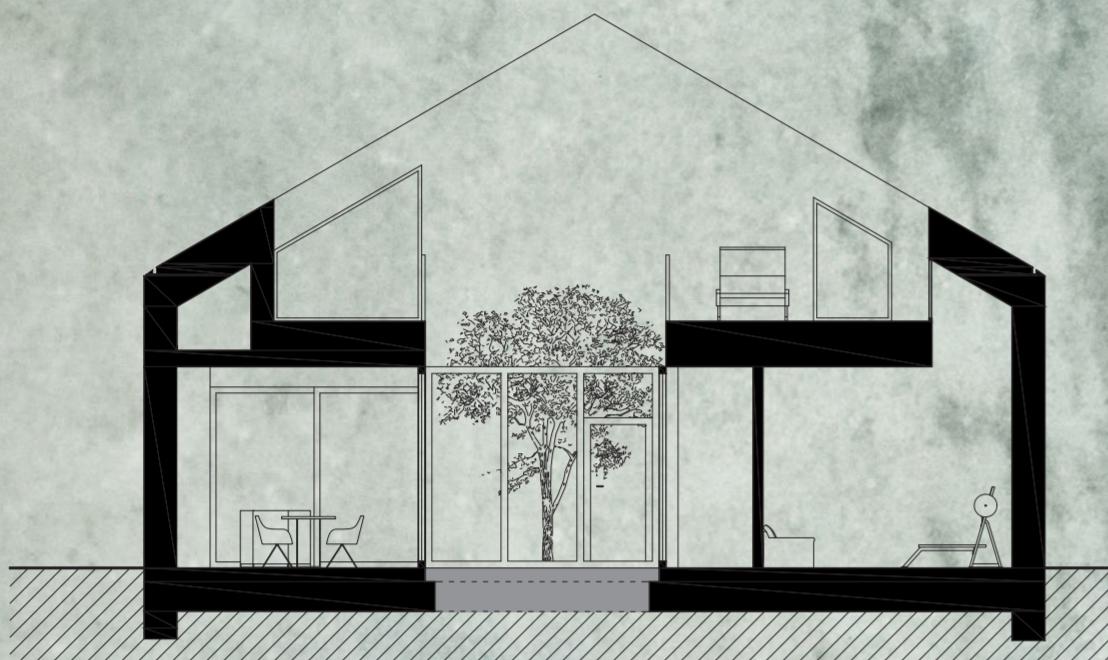

Sezione B-B scala 1:100

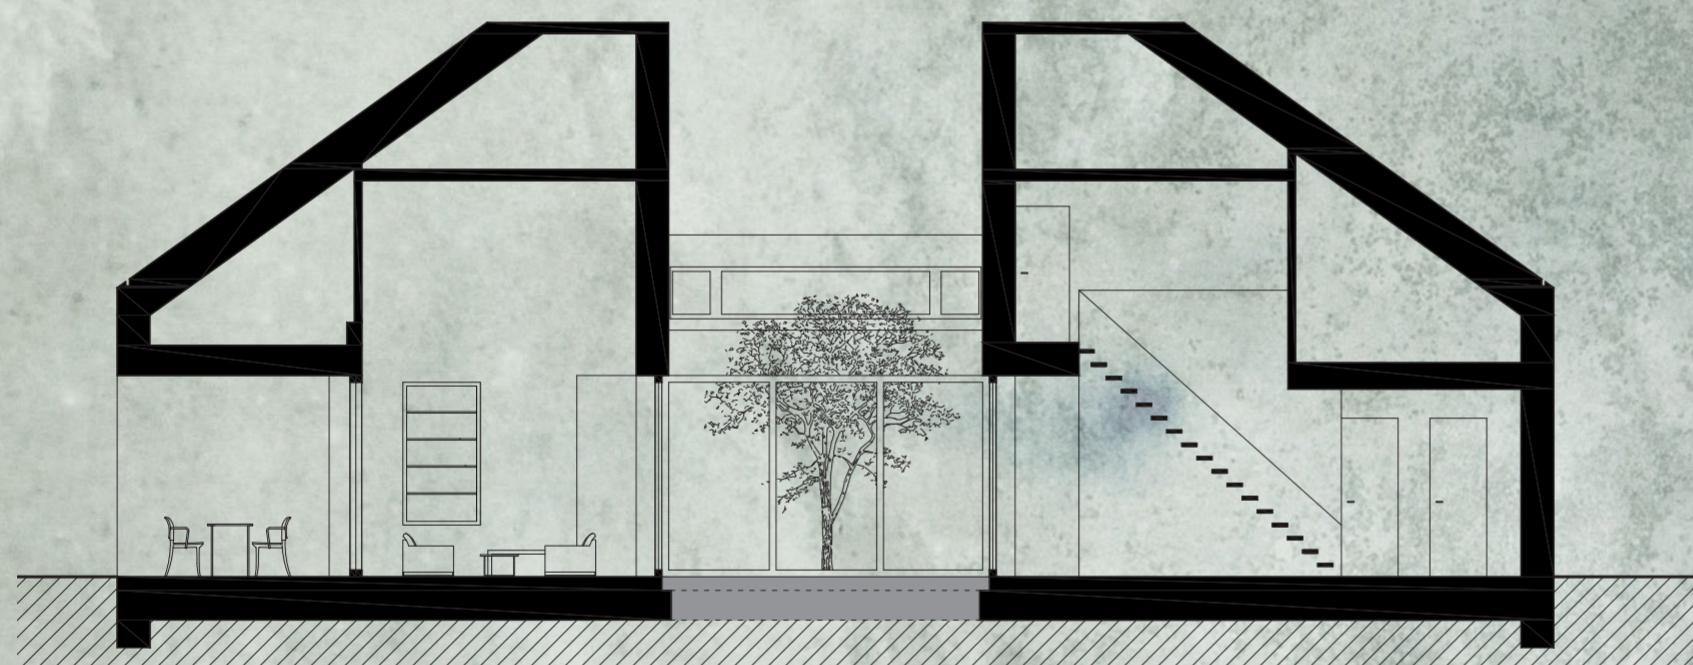

Sezione A-A scala 1:100

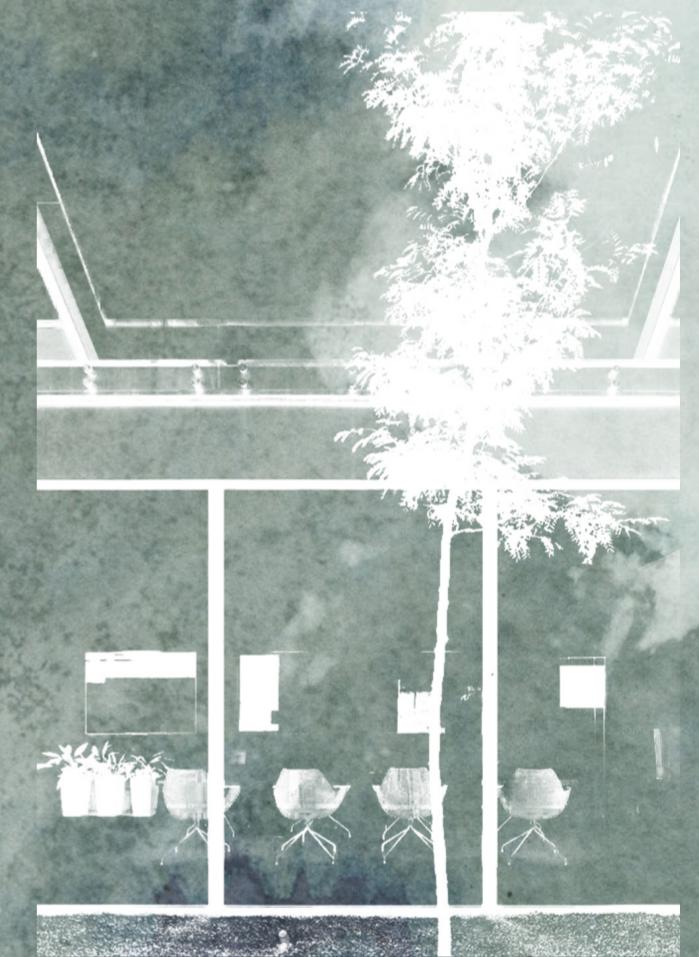



Rielaborazione grafica della serra




Rielaborazione grafica della zona living






Rielaborazione grafica della serra

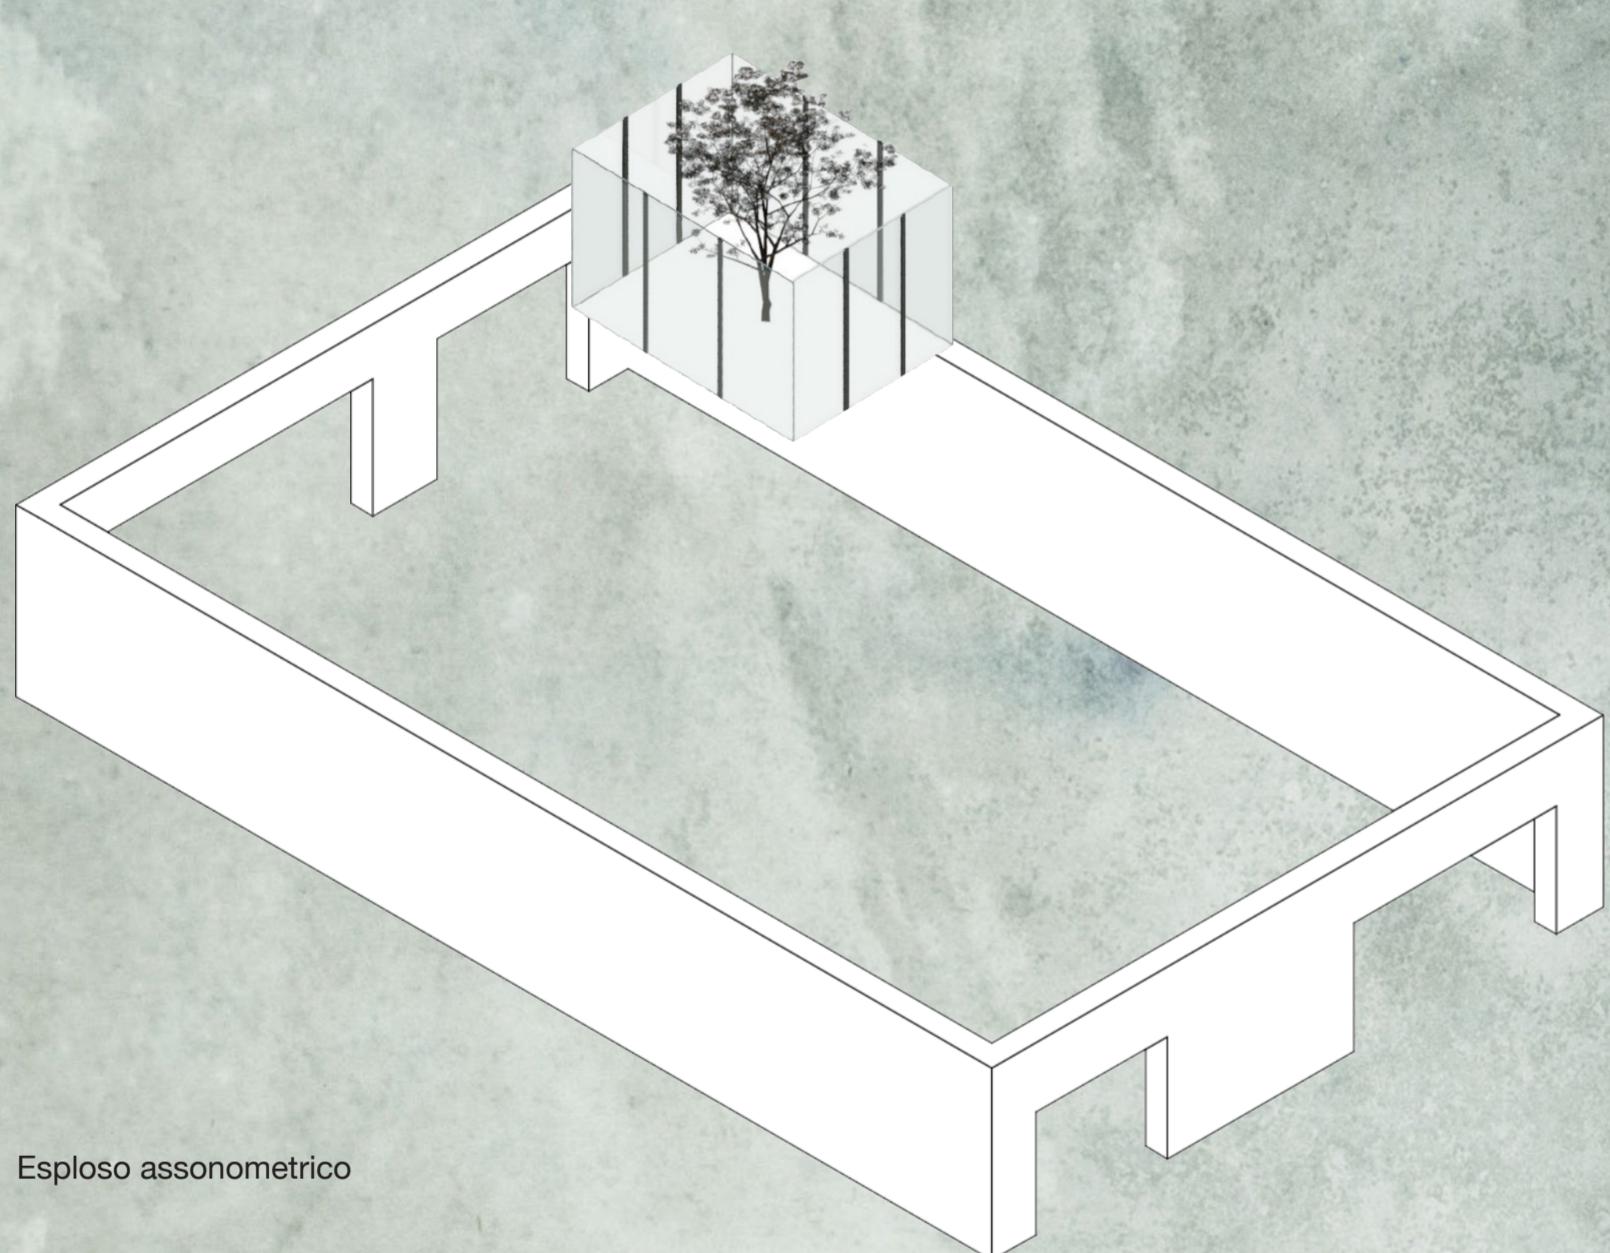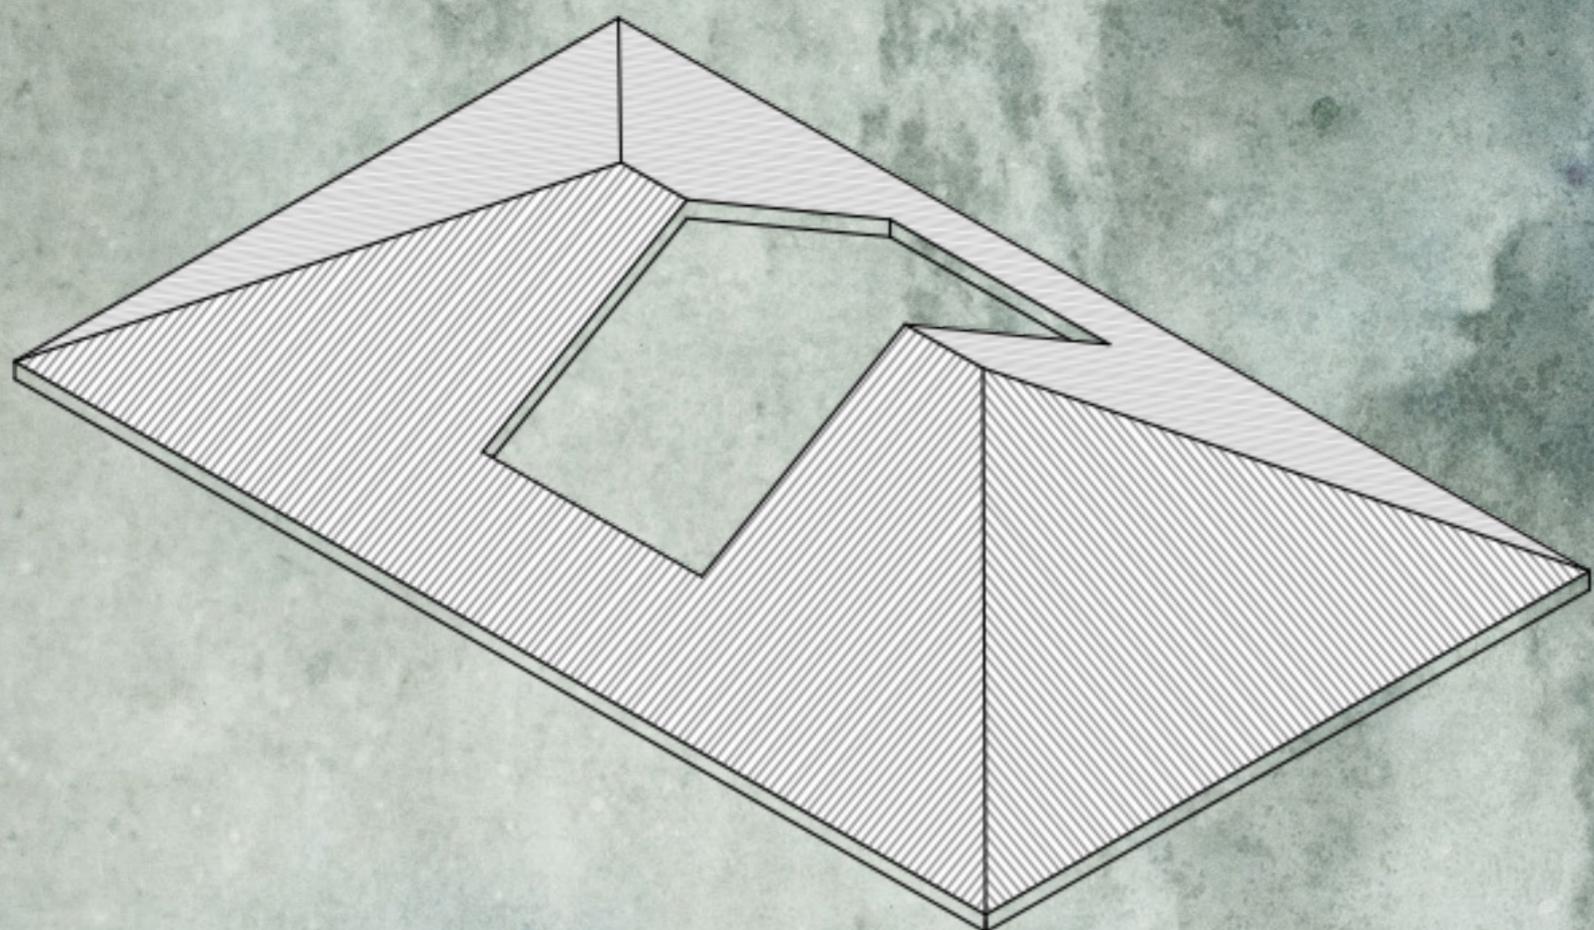

Esploso assonometrico

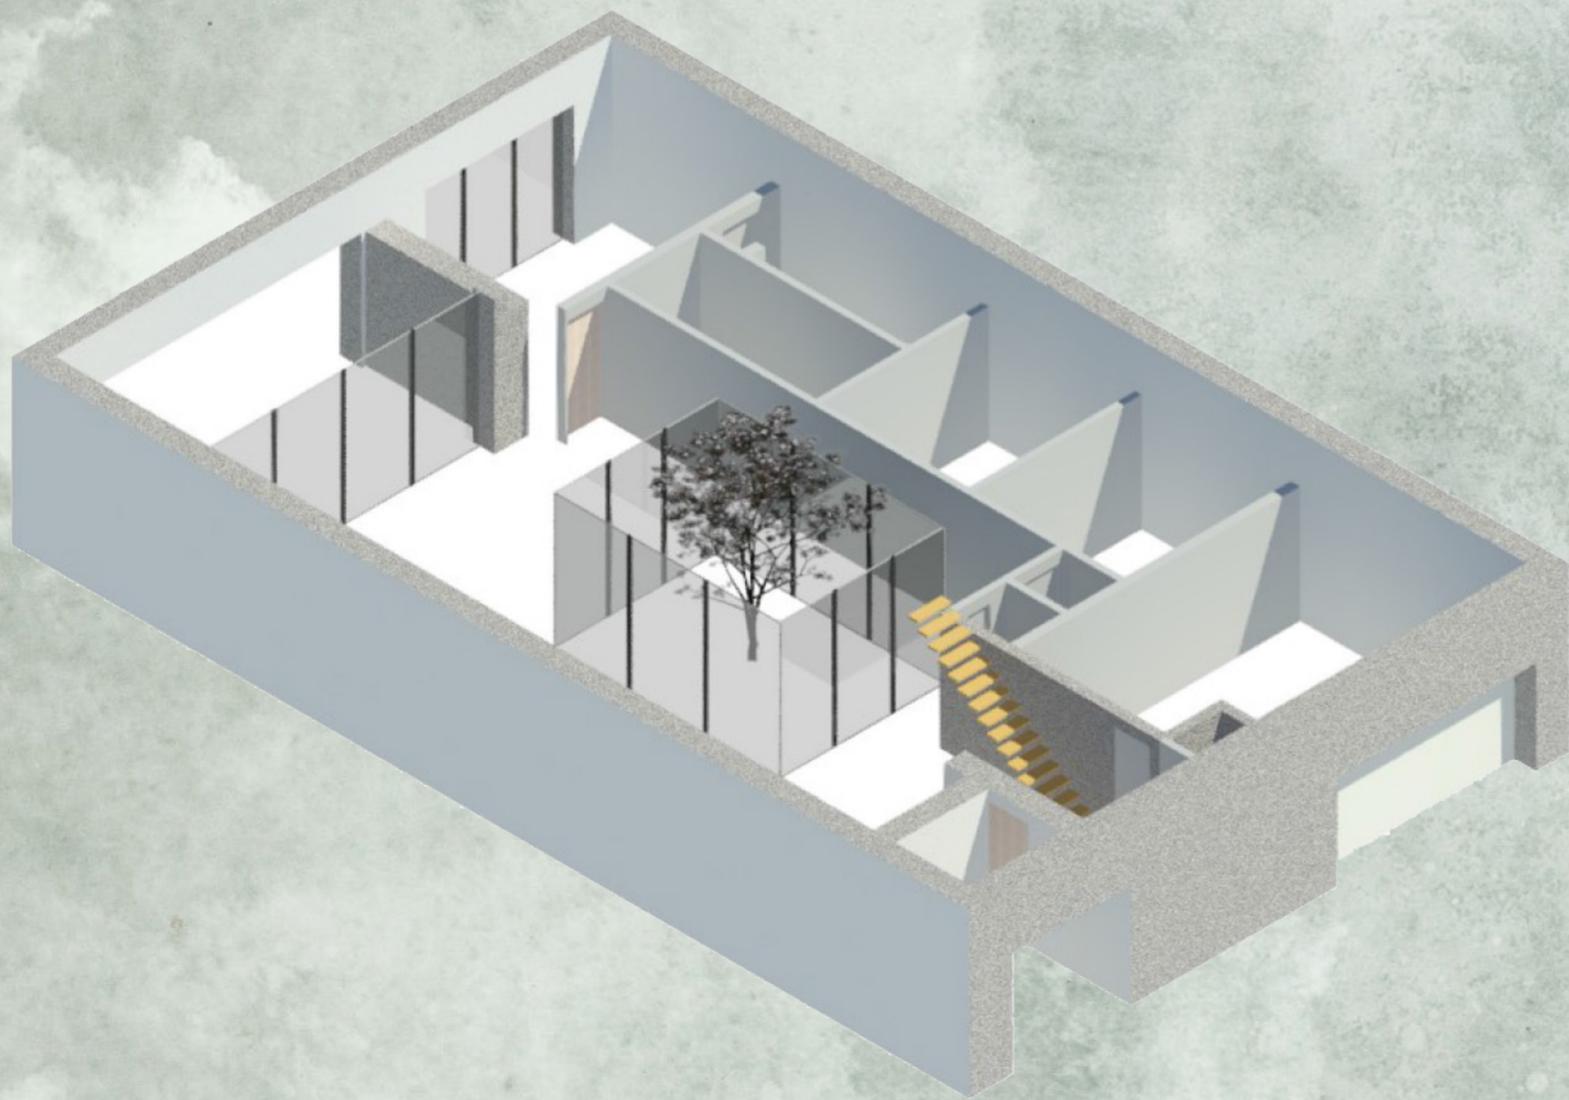

Vista assonometriche dell'interno

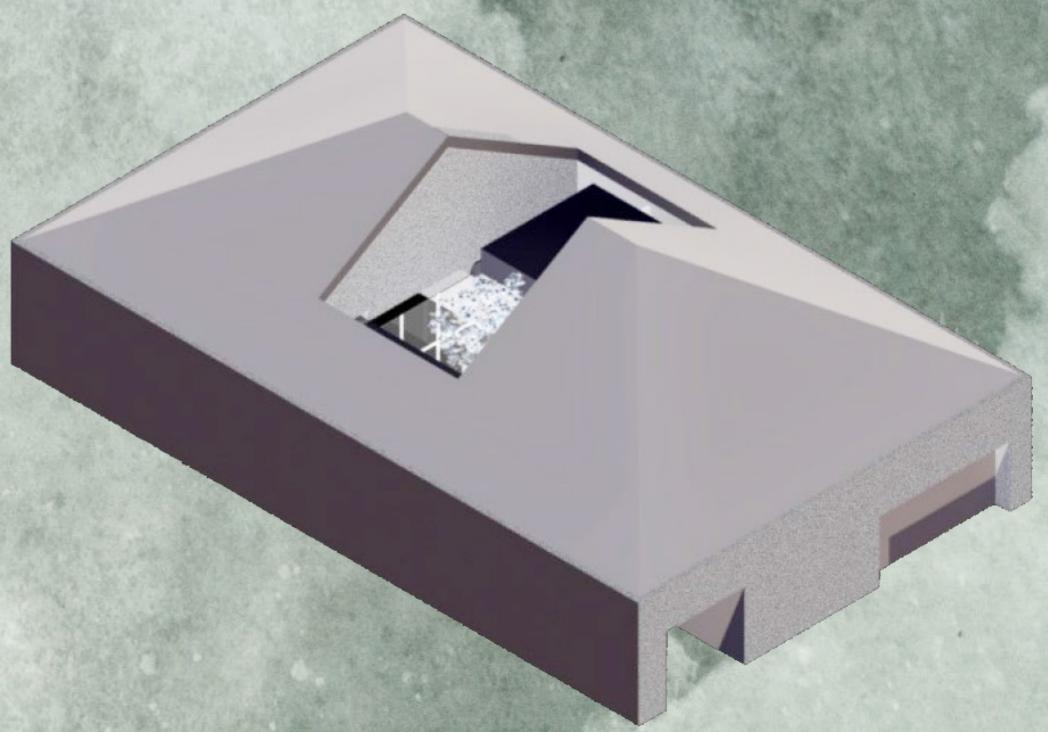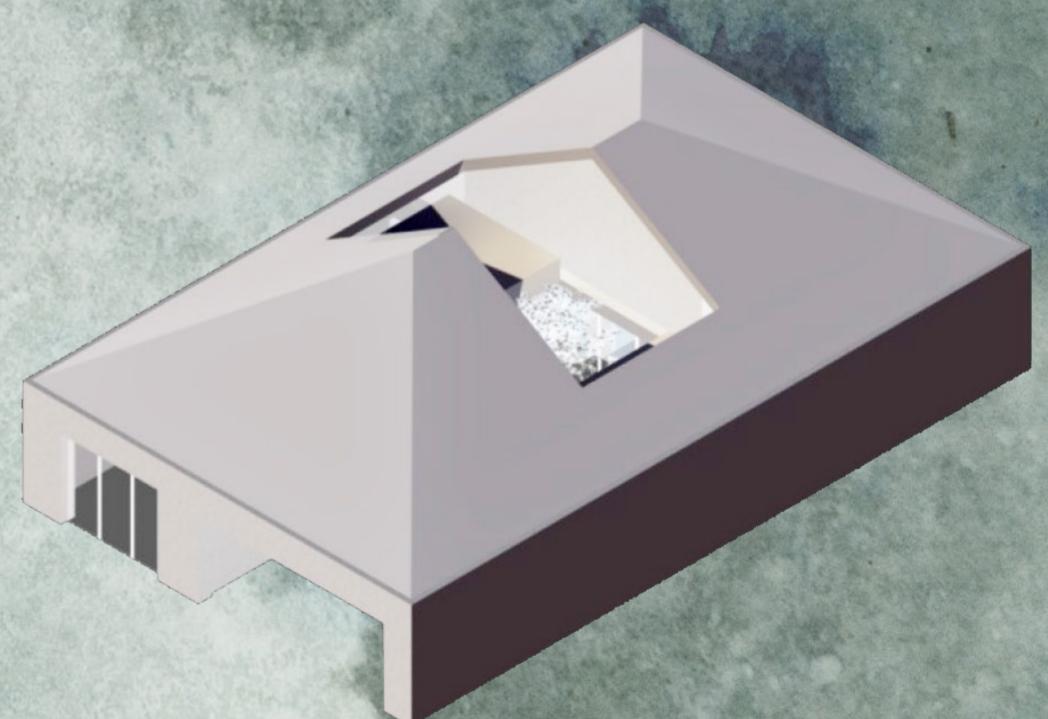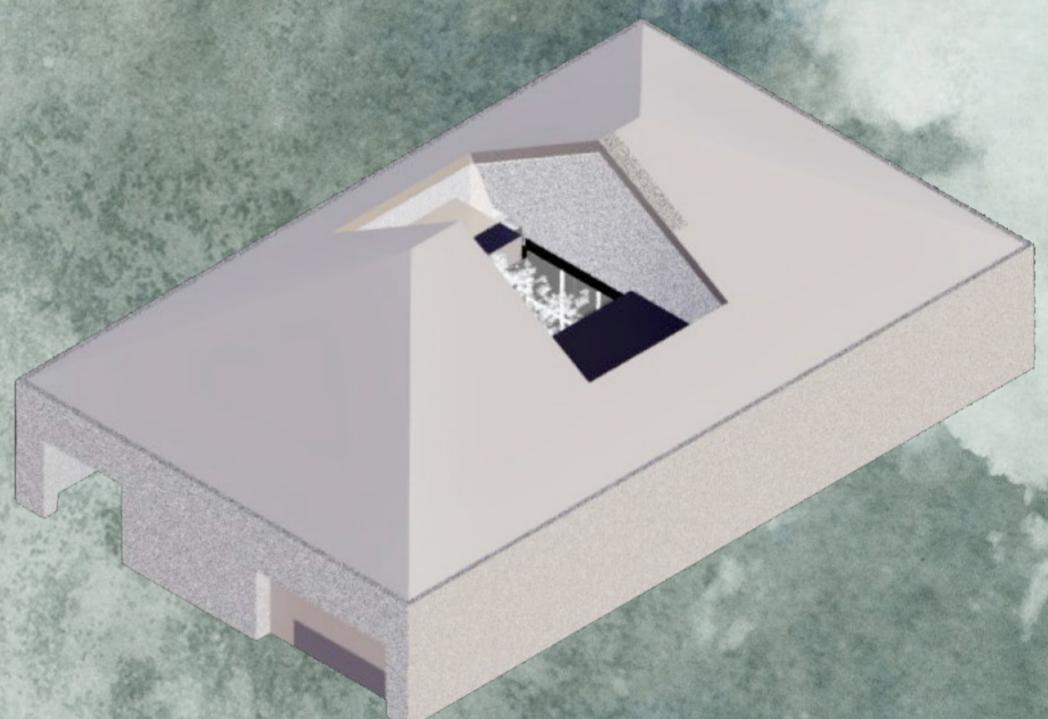

Viste assonometriche dell'architettura